

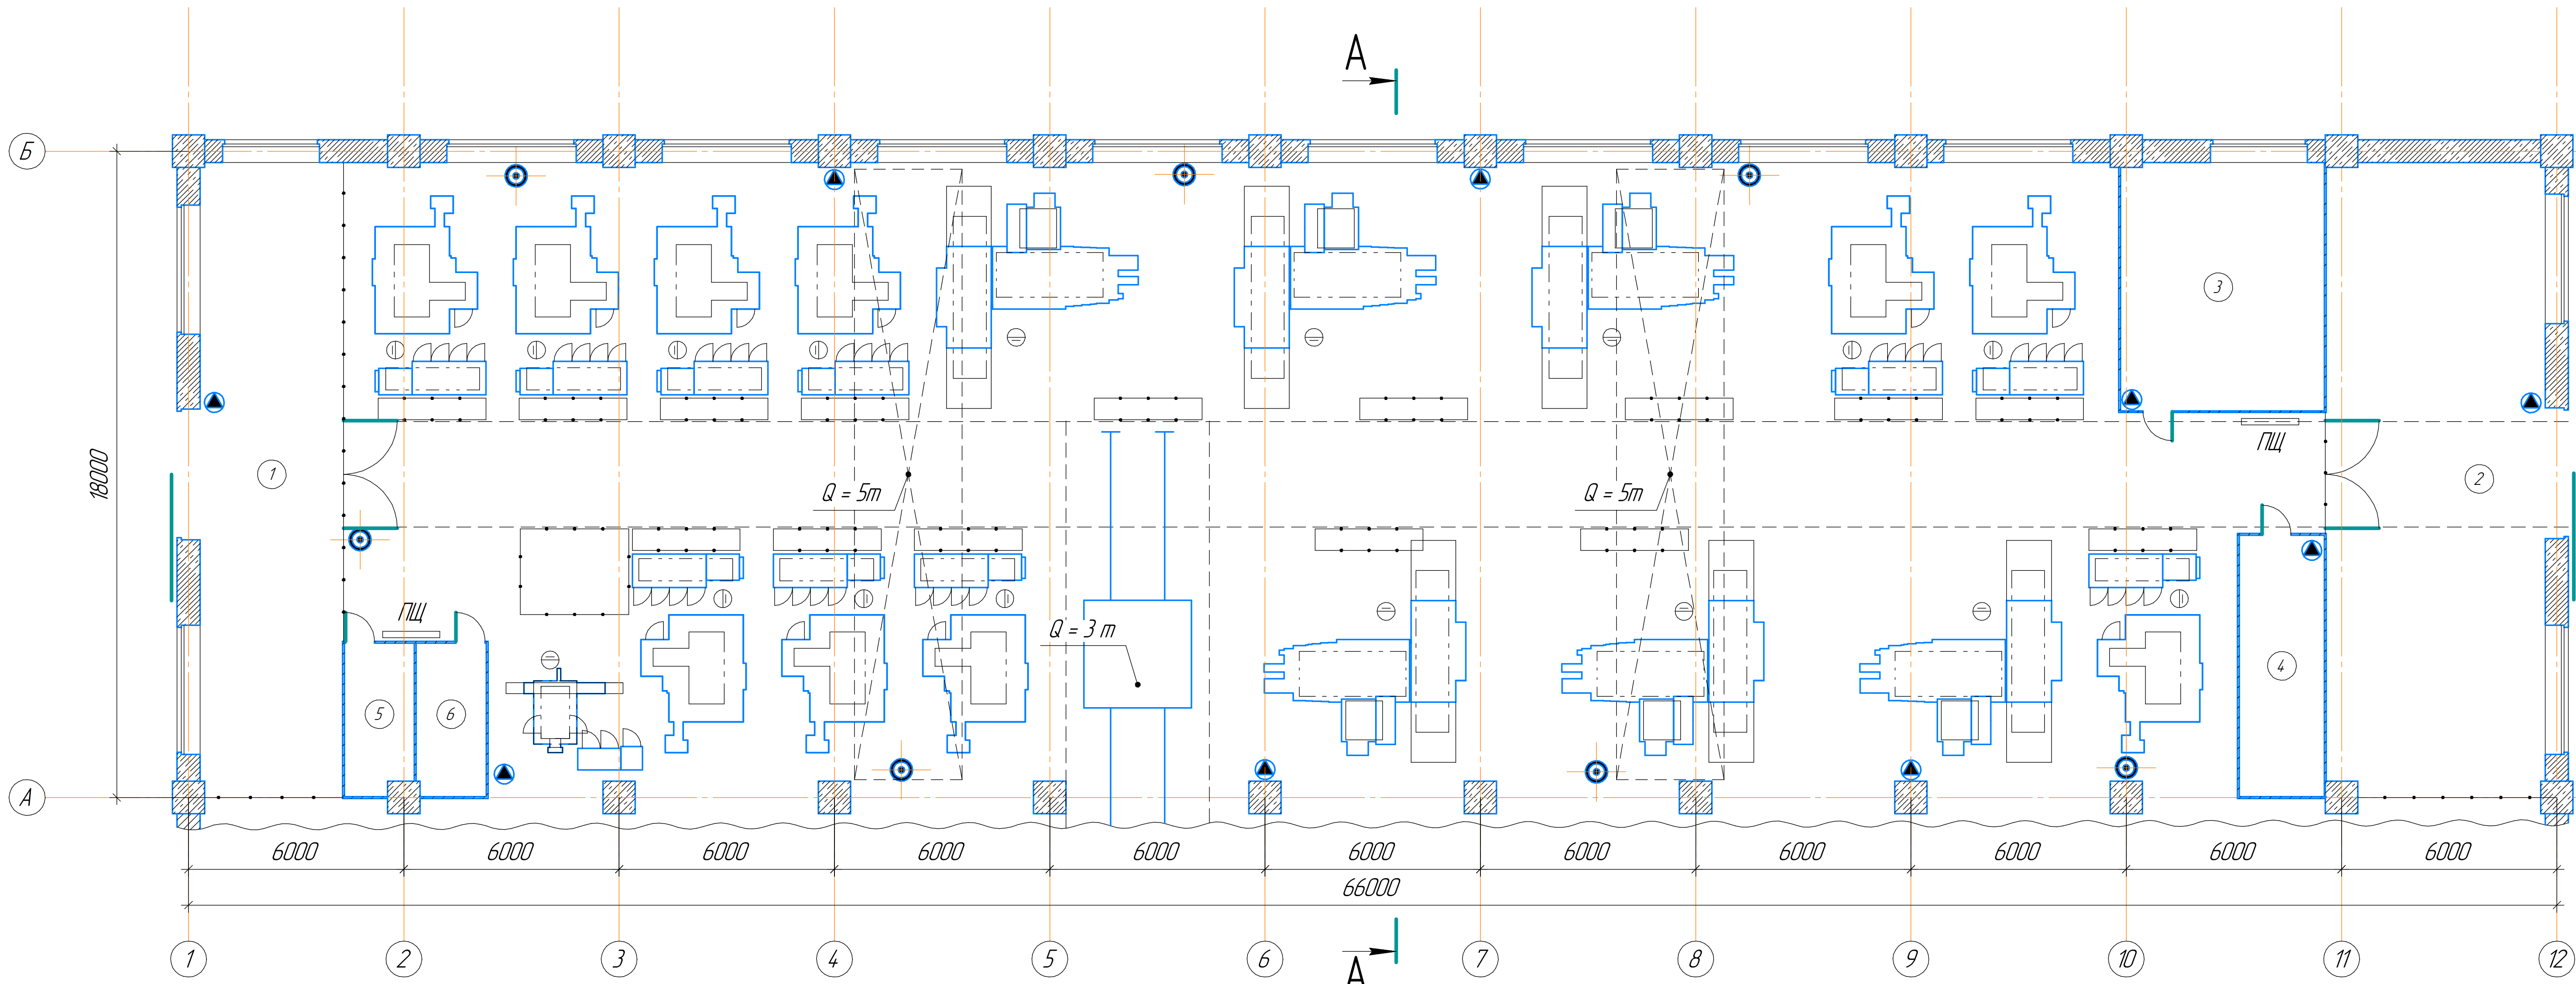


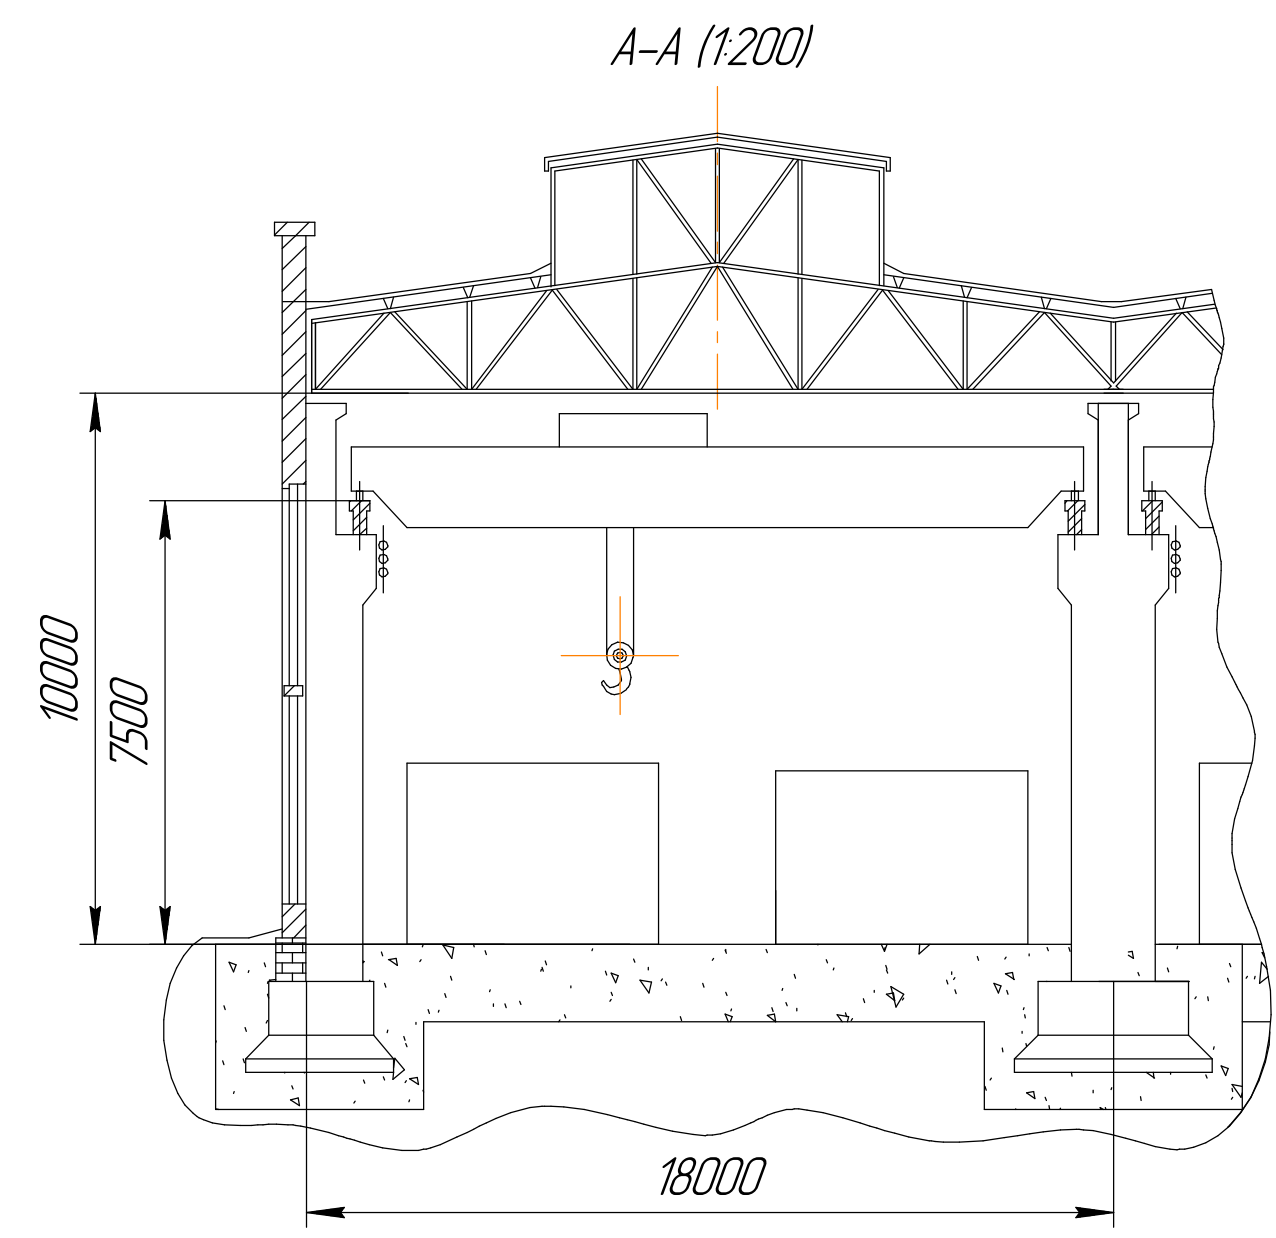

Условные обозначения:

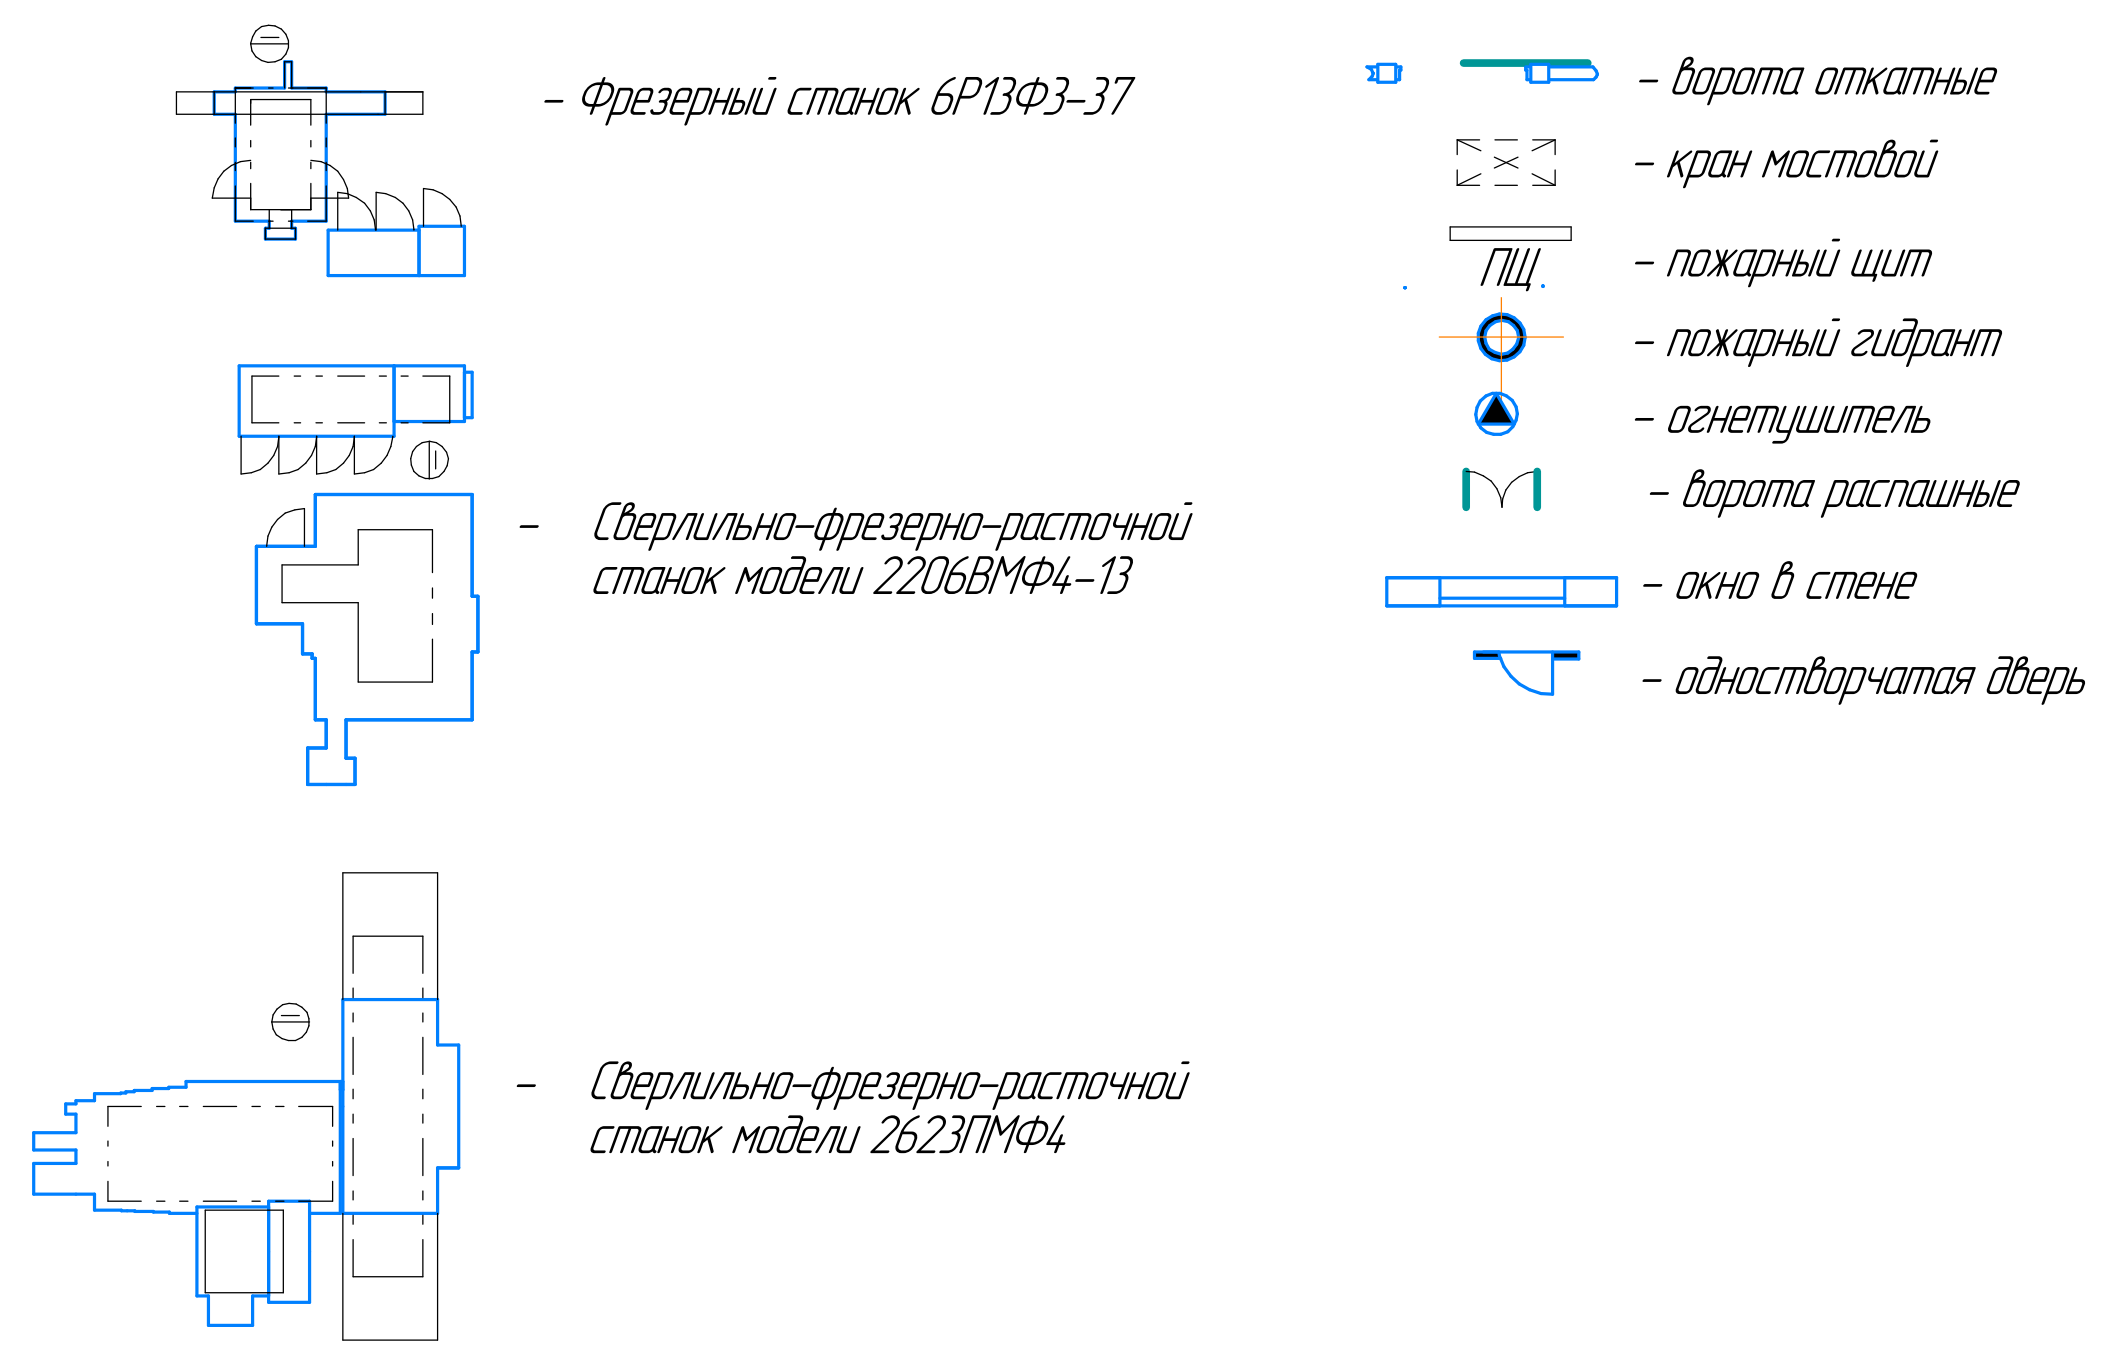

Наименование	Площадь, м ²	Кат. помещения
1. Склад материалов и заготовок	70,54	
2. Склад готовых деталей	107,44	
3. Контрольное отделение	39,2	
4. Инструментально-раздаточная кладовая	17,28	
5. Сан.узел женский	8,01	
6. Сан.узел мужской	8,28	

711219-Цех 00-2112-TX.03.00				Лист	Масса	Масштаб
Участок механической обработки				1	-	1:100
000 «Криво, Но Подтягиваю»				Лист	Листов	1
Формат А1				Копировал		