



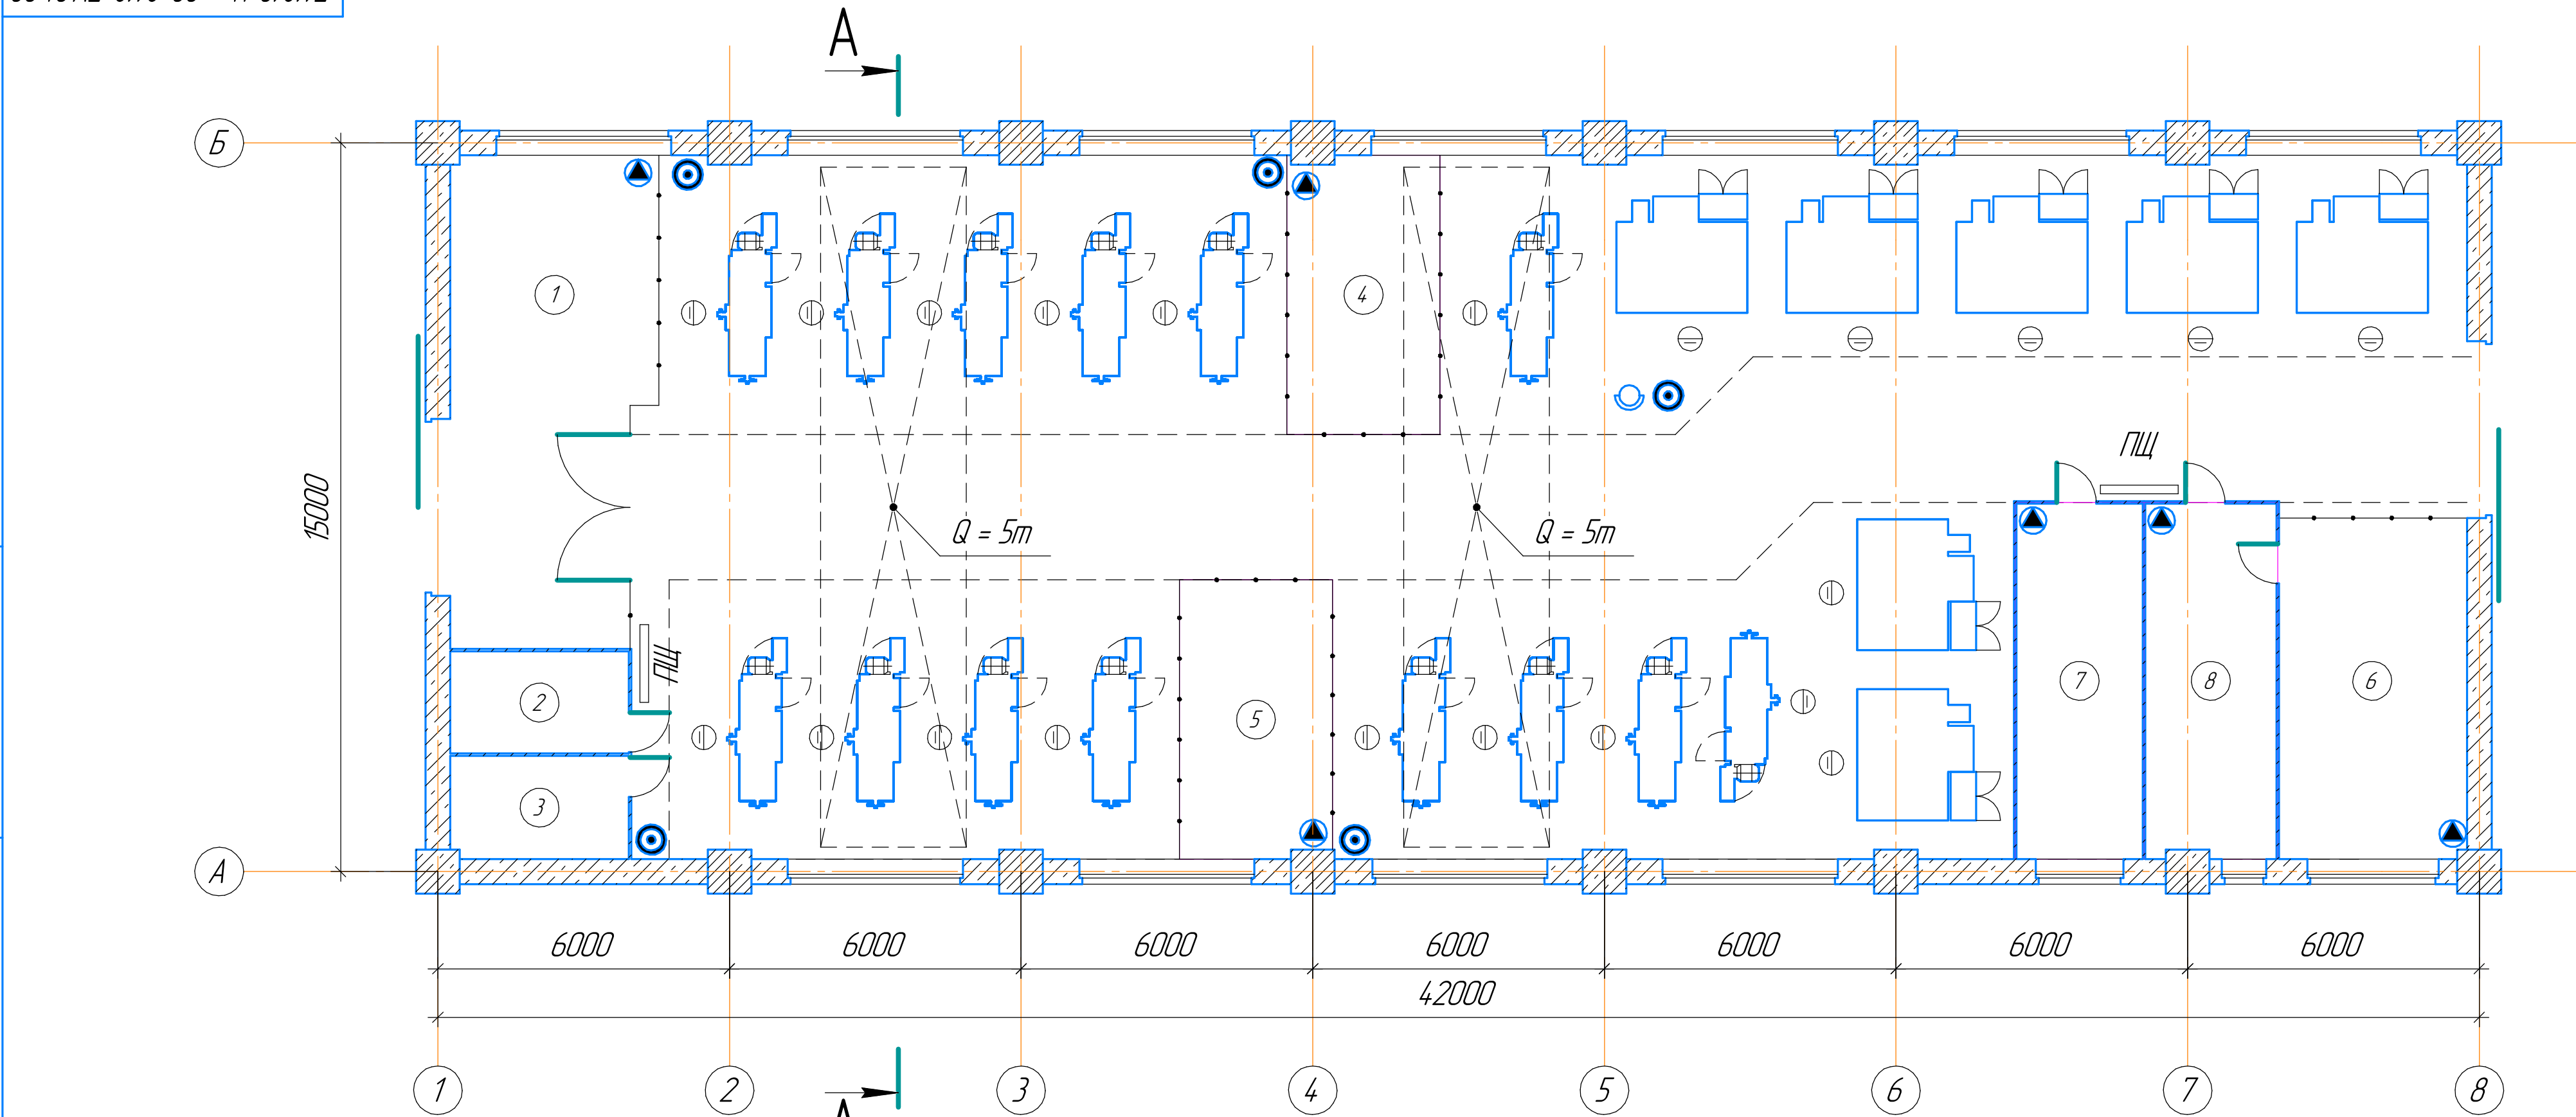

A-A (1:200)

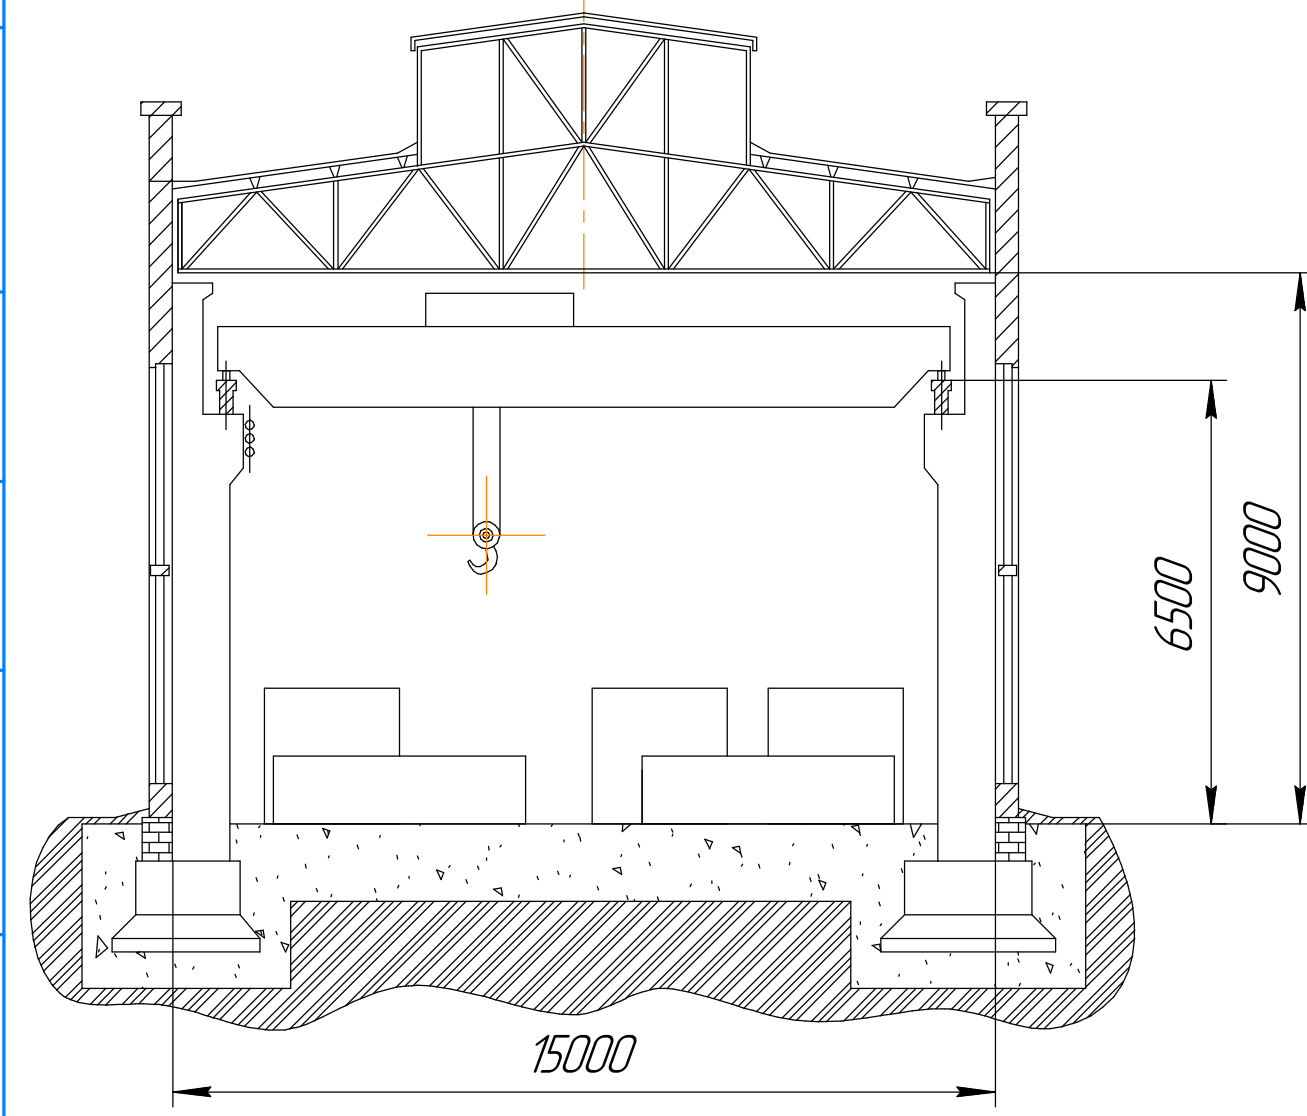

Условные обозначения:

- ворота откатные
- кран мостовой
- ПЩ — пожарный щит
- пожарный гидрант
- огнетушитель
- ворота распашные
- окно в стене
- одностворчатая дверь
- Токарный станок 16К20ПМ
- Обрабатывающий центр 600V

Номер помещения	Наименование	Площадь, м ²	Кат. помещения
1	Склад материалов и заготовок	40,96	
2	Санитарный узел (М)	7,72	
3	Санитарный узел (Ж)	7,77	
4	Склад межоперационных деталей	17,94	
5	Склад межоперационных деталей	17,95	
6	Склад готовых деталей	27,13	
7	Инструментально-раздаточная кладовая	19,03	
8	Контрольное отделение	19,58	

71219-Цех 00-2112-ТХ.04.00				Лит.	Масса	Масштаб
Цех механической обработки						1:1
Изм./Лист	№ докум.	Подп.	Дата	Лист	Листов	1
Разраб.						
Пров.						
Т.контр.						
Н.контр.						
Утв.						
000 «Чертеж Потек»				Формат	А2	