
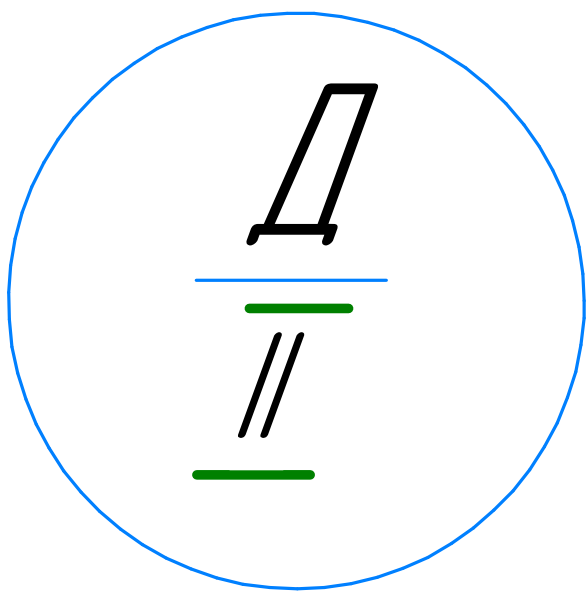


Участок механической обработки деталей "Вал муфты привода вентилятора"

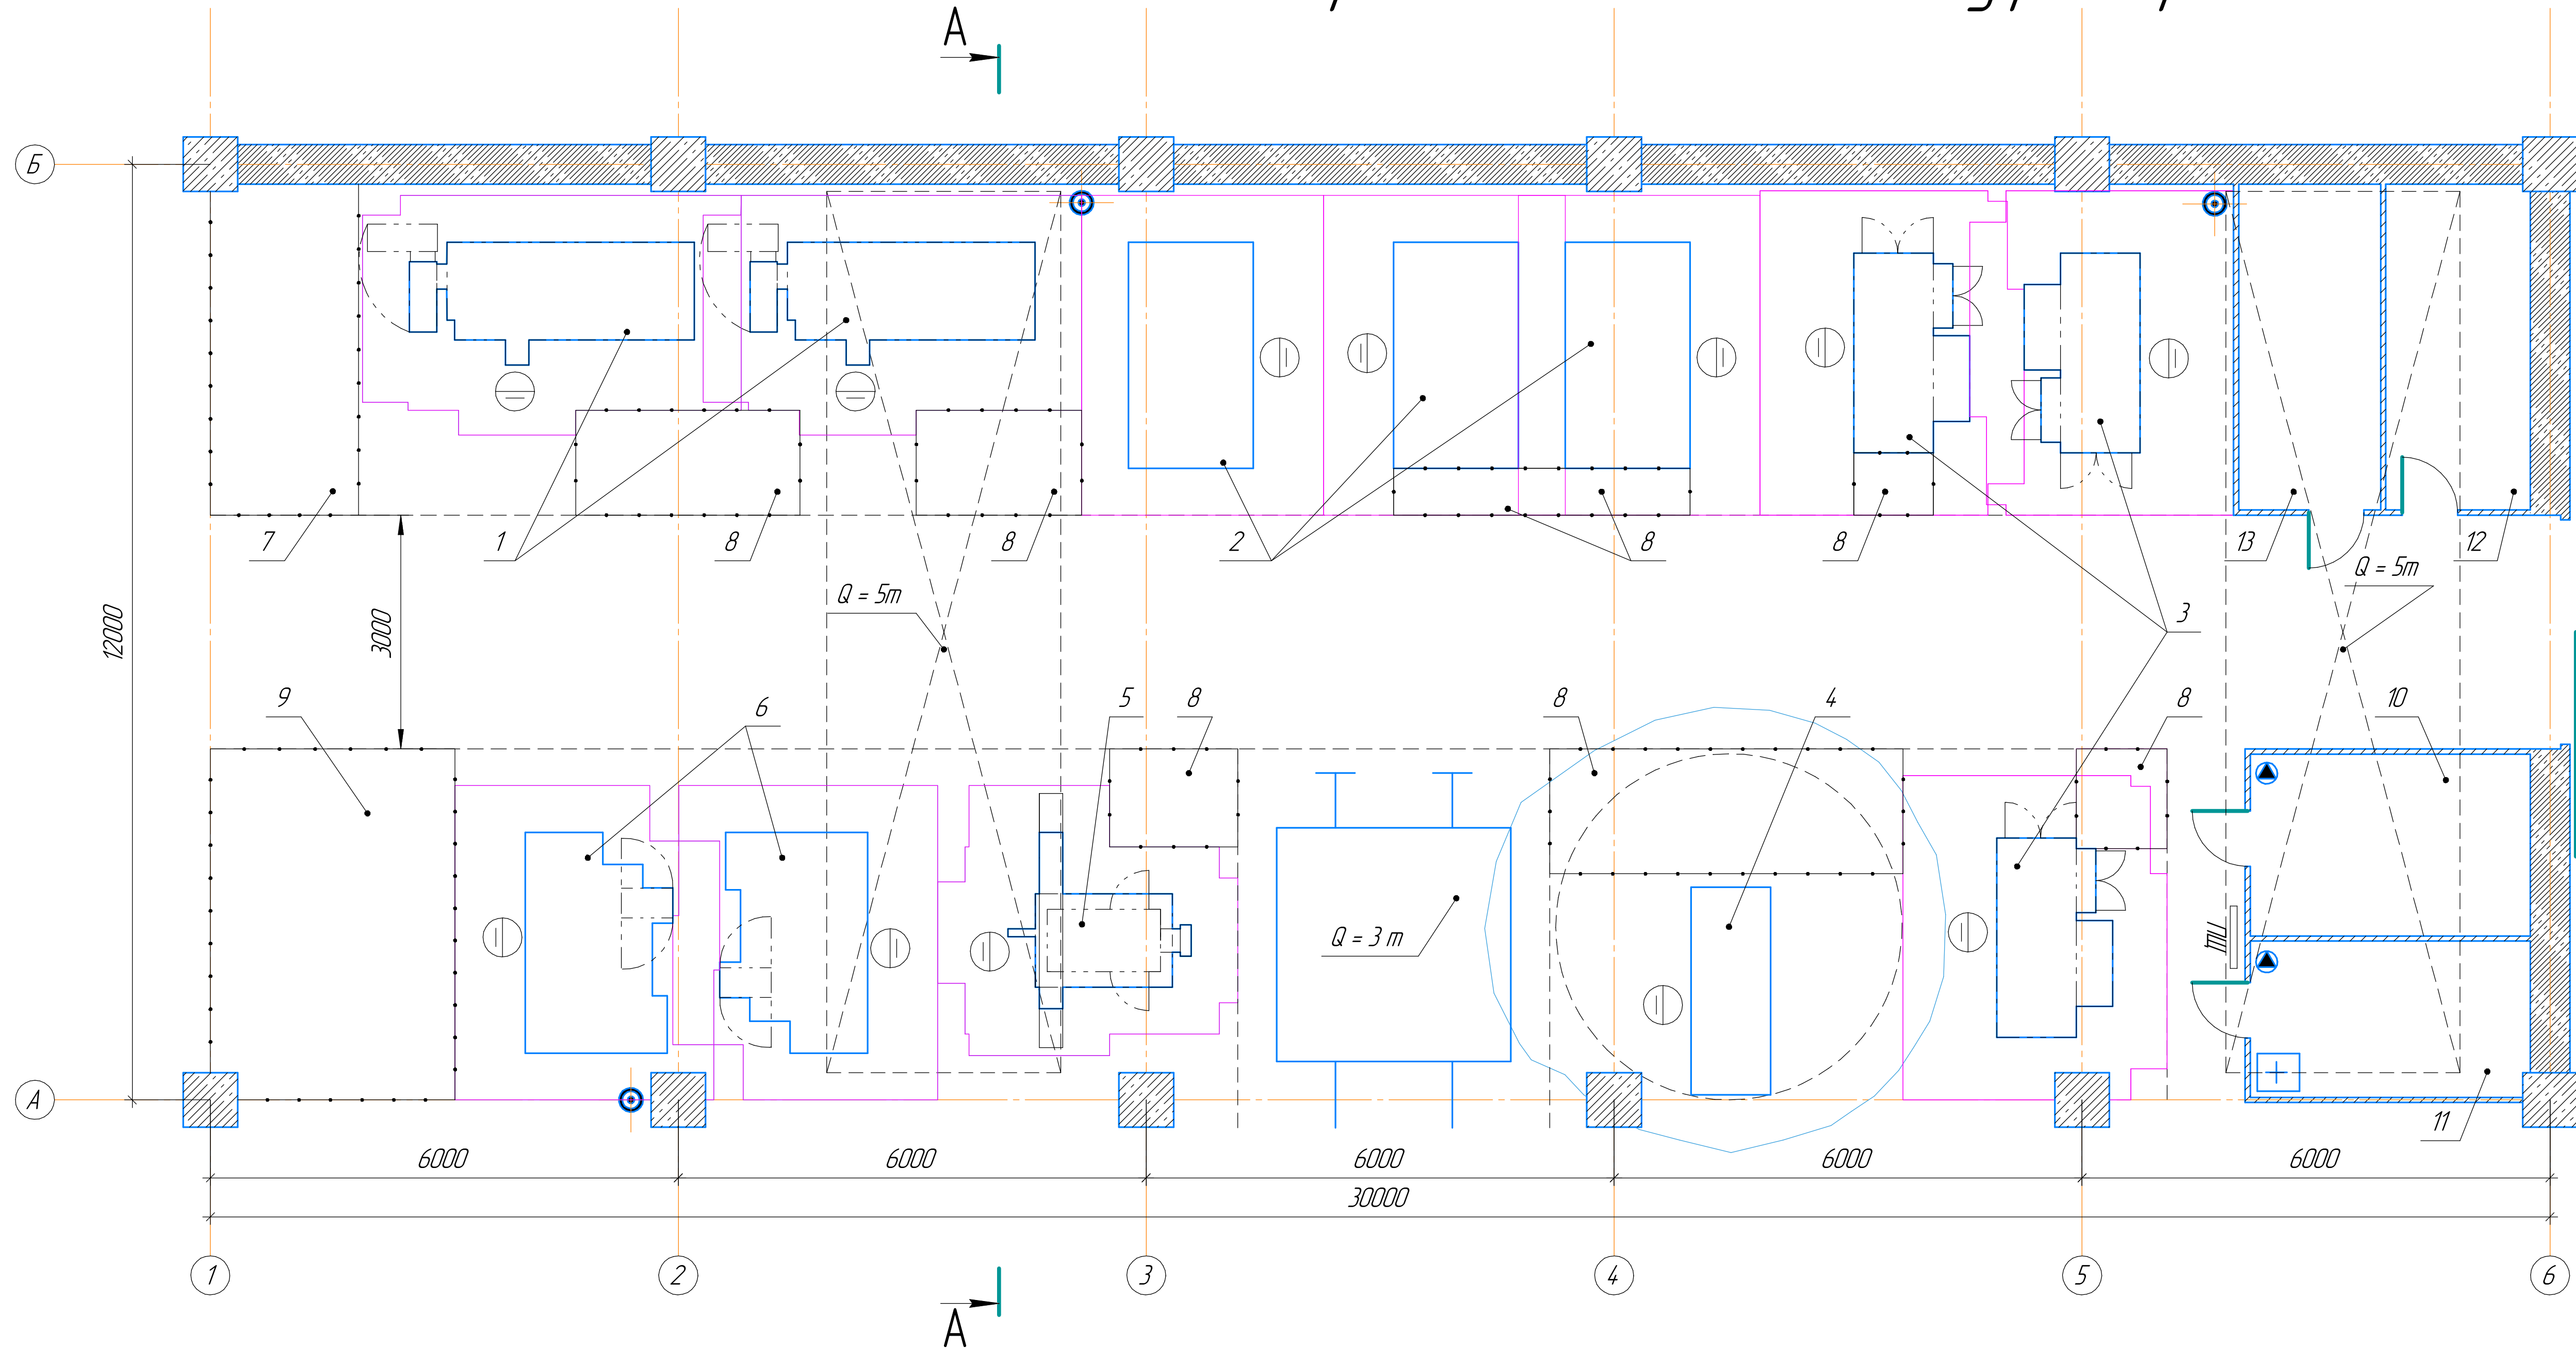

А-А
(1:100)


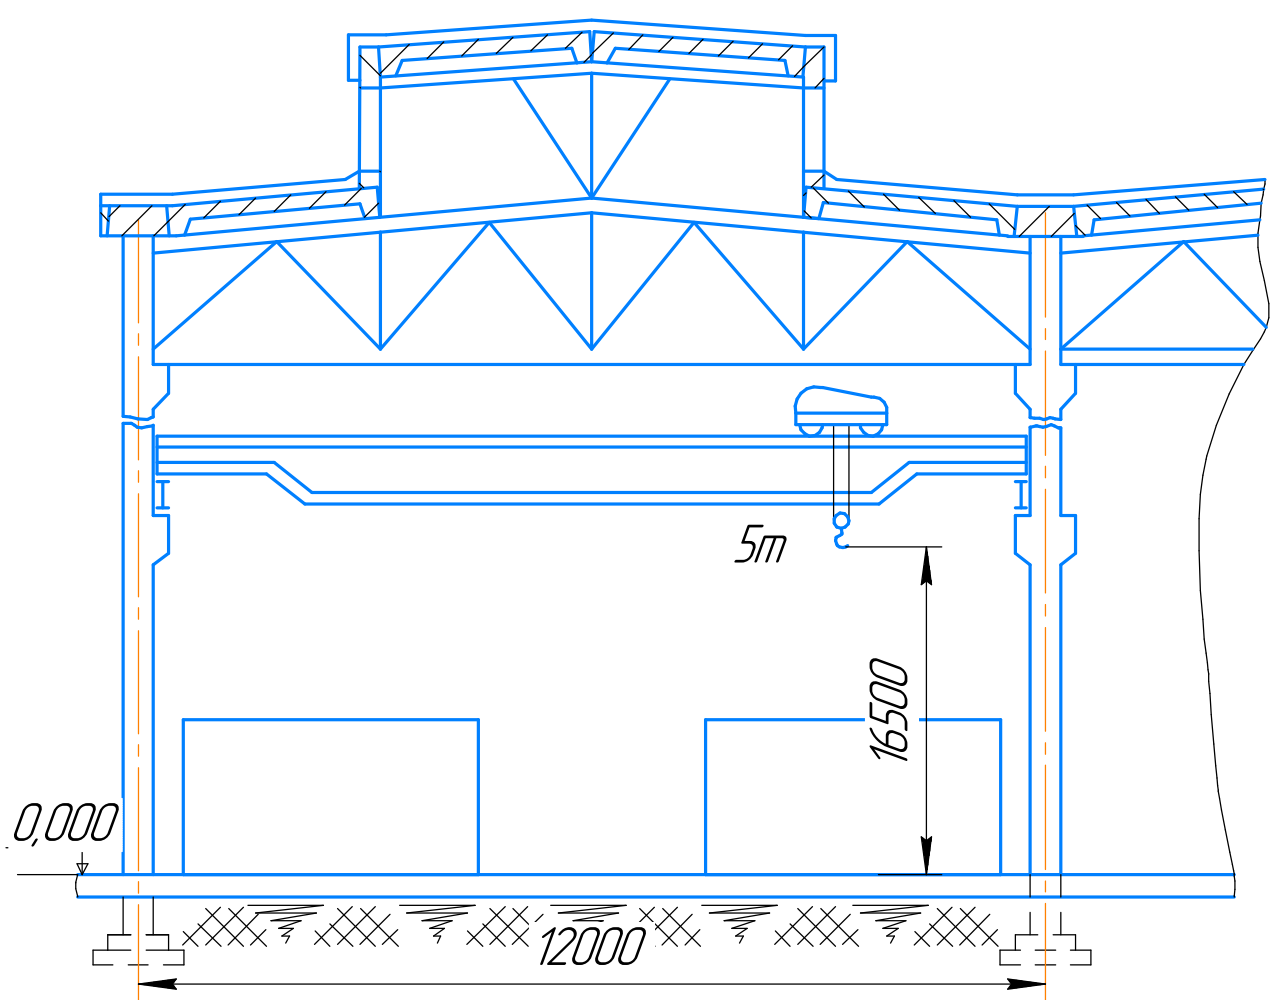


График загрузки станка на участке

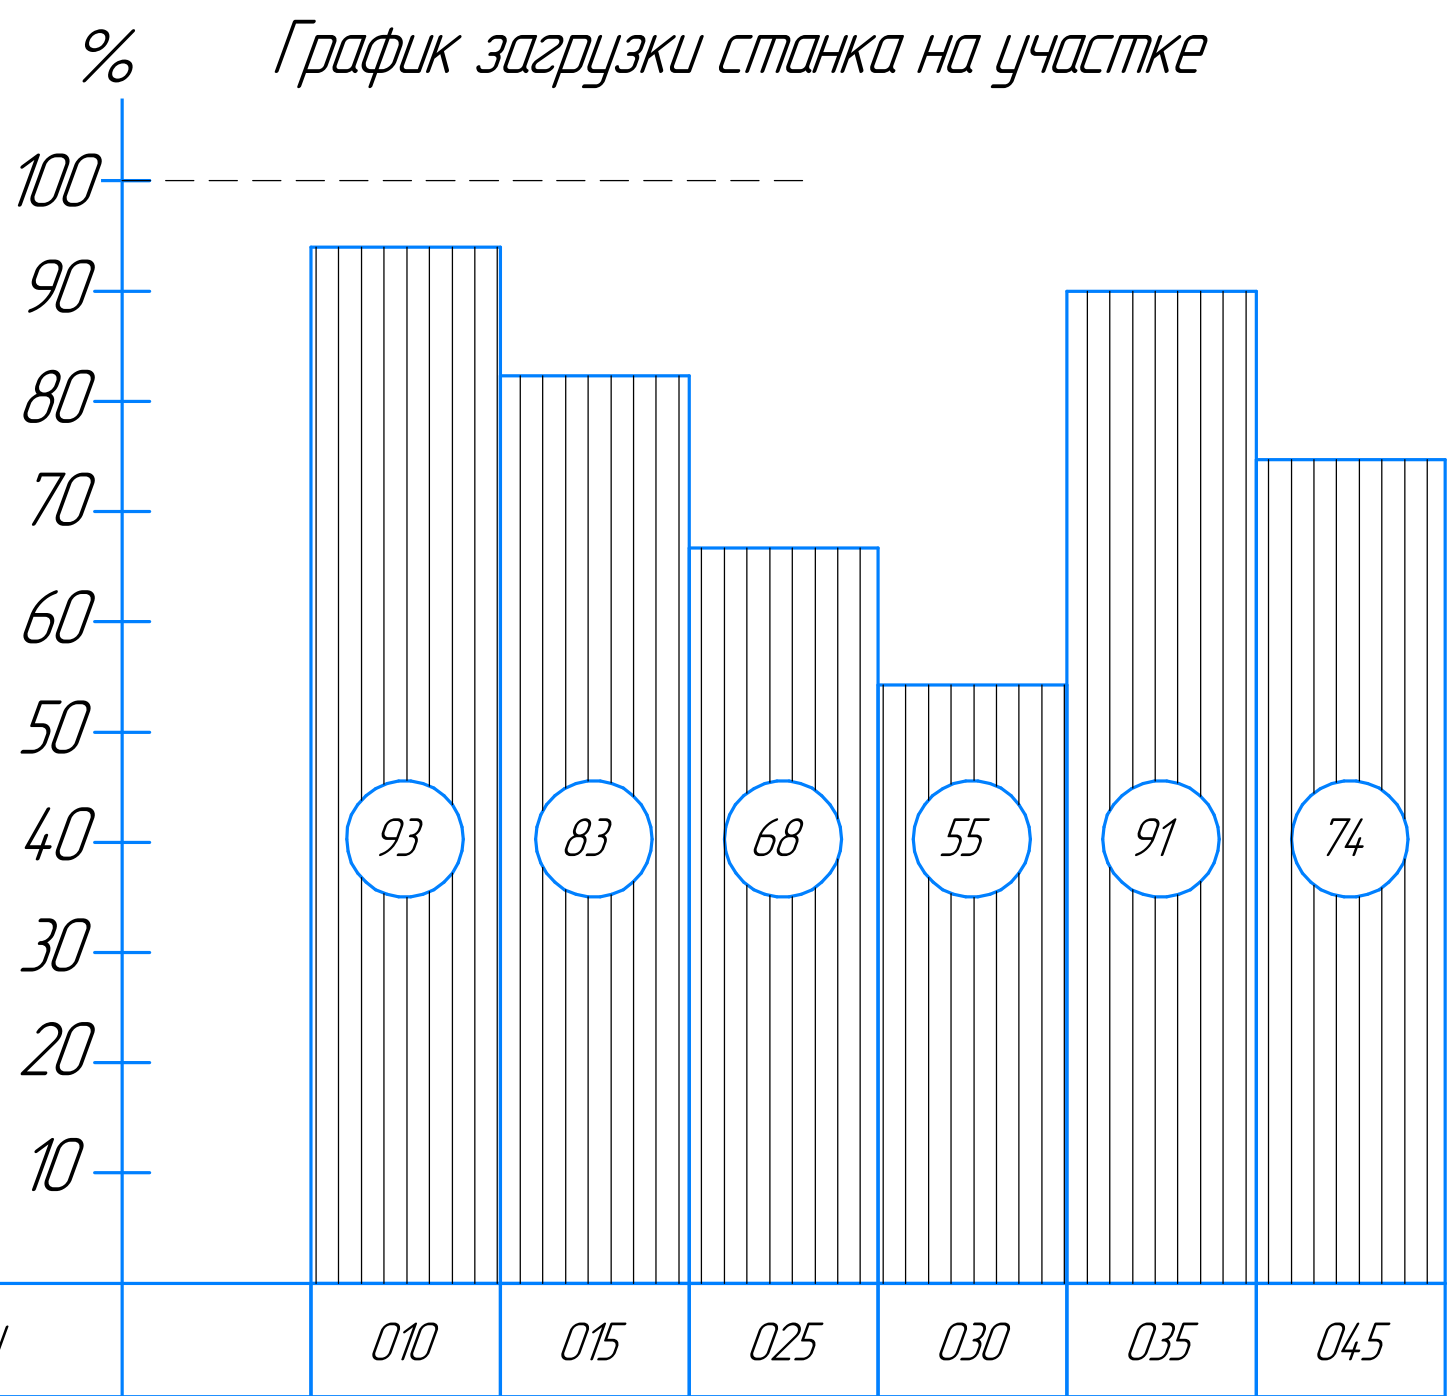

Условные обозначения:

- ворота откатные
- кран мостовой
- ПЩ
- пожарный гидрант
- огнетушитель
- ворота распашные
- окно в стене
- одностворчатая дверь
- оплечка
- рабочее место станочника

- 1 - Фрезерно-центровальный станок модели МР - 78
- 2 - Станок токарный с ЧПУ с противопинделем С-200ТСМ
- 3 - Зубофрезерный станок модели 53А11
- 4 - Радиально-сверлильный станок модели 2М55
- 5 - Вертикально-фрезерный станок модели 6Р13Ф3
- 6 - Круглошлифовальный станок модели 3М174
- 7 - Склад заготовок
- 8 - Склад промежуточных деталей
- 9 - Склад готовой продукции
- 10 - Контрольное отделение
- 11 - Инструментально-раздаточная кладовая
- 12 - Санузел муж.
- 13 - Санузел жен.

711219-Цех 00-2112-TX.05.00				Лист	Масштаб
Планировка участка механической обработки				-	1:50
Изм. Лист	№ докум.	Подп.	Дата	Лист	Листов
Разраб.					1
Проб.					
Т.контр.					
Н.контр.					
Утв.					
ООО «Линейный Болт»				Не Помешает	
Копировал				Формат А1	