


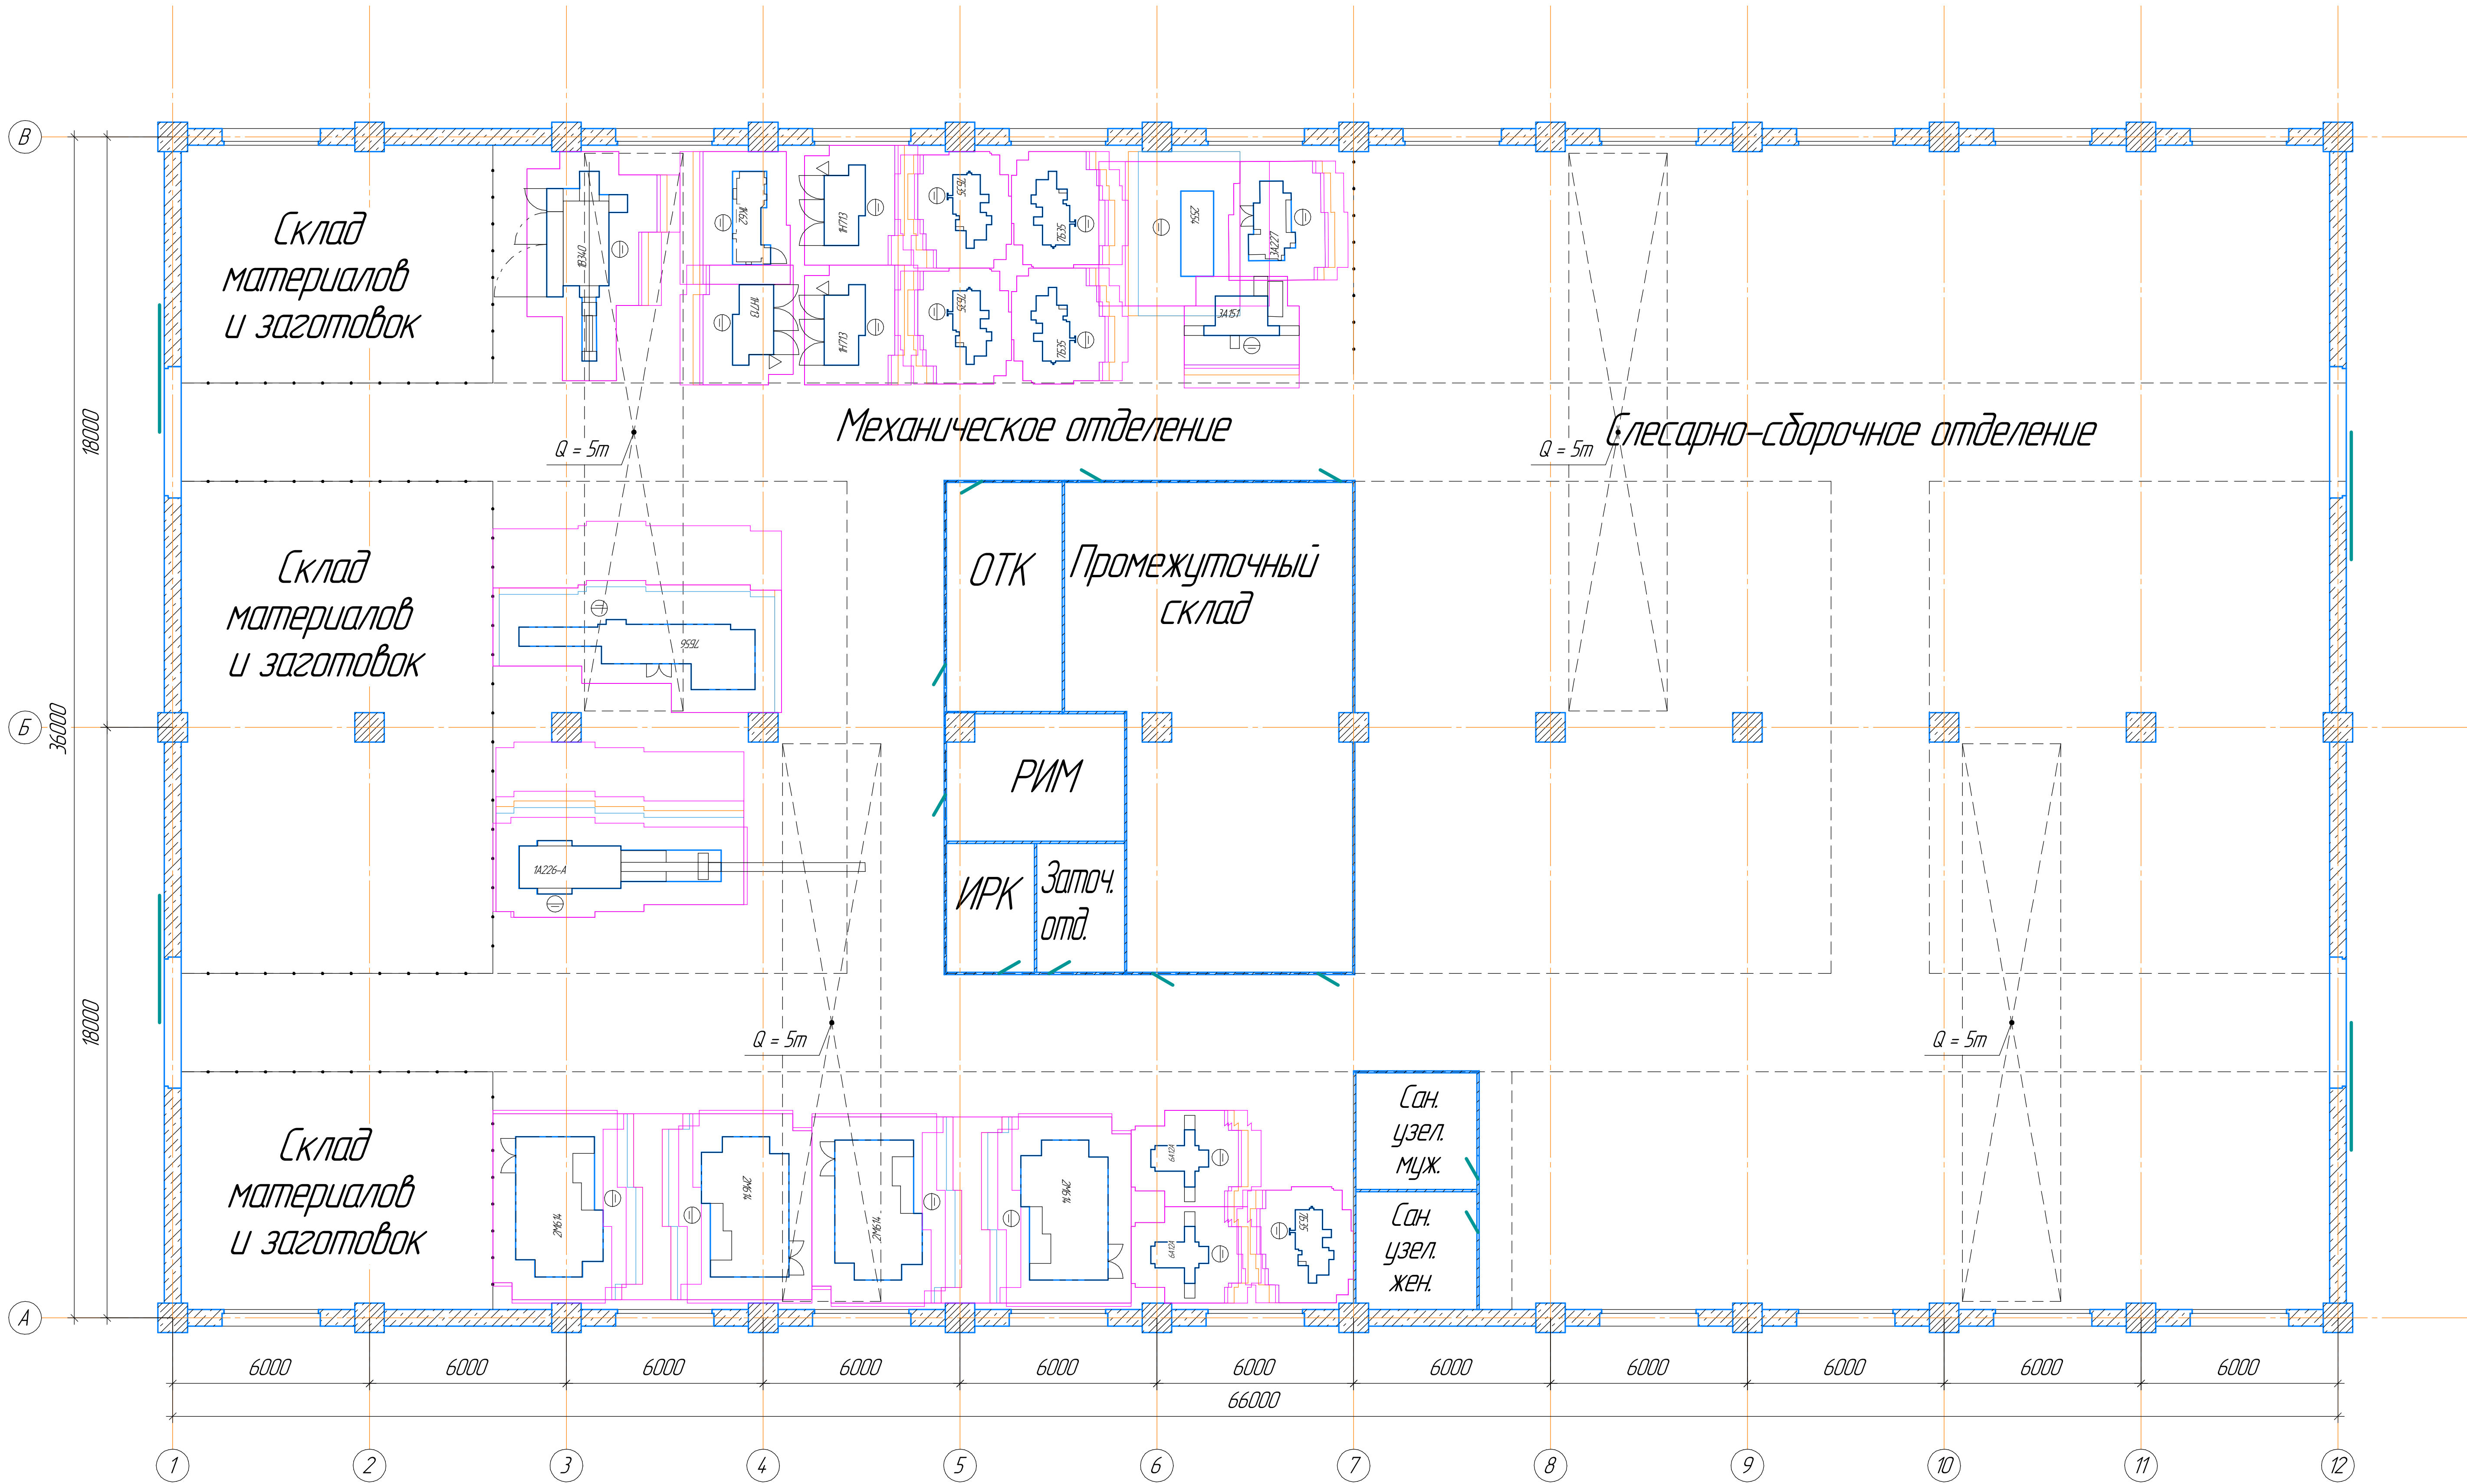

Условные обозначения

- Ворота откатные
- Ограждения
- Окно
- Проход или проезд
- Дверь
- Кран мостовой

					711219-Цех 00-2112-TX.09.00					
					Проект механосборочного цеха			Лит.	Масса	Масштаб
Изм.	Лист	№ докум.	Подп.	Дата				Лист	Листов	1
Разраб.										
Проб.										
Т.контр.										
Н.контр.					ООО «Завинти и забудь»					
Утв.										