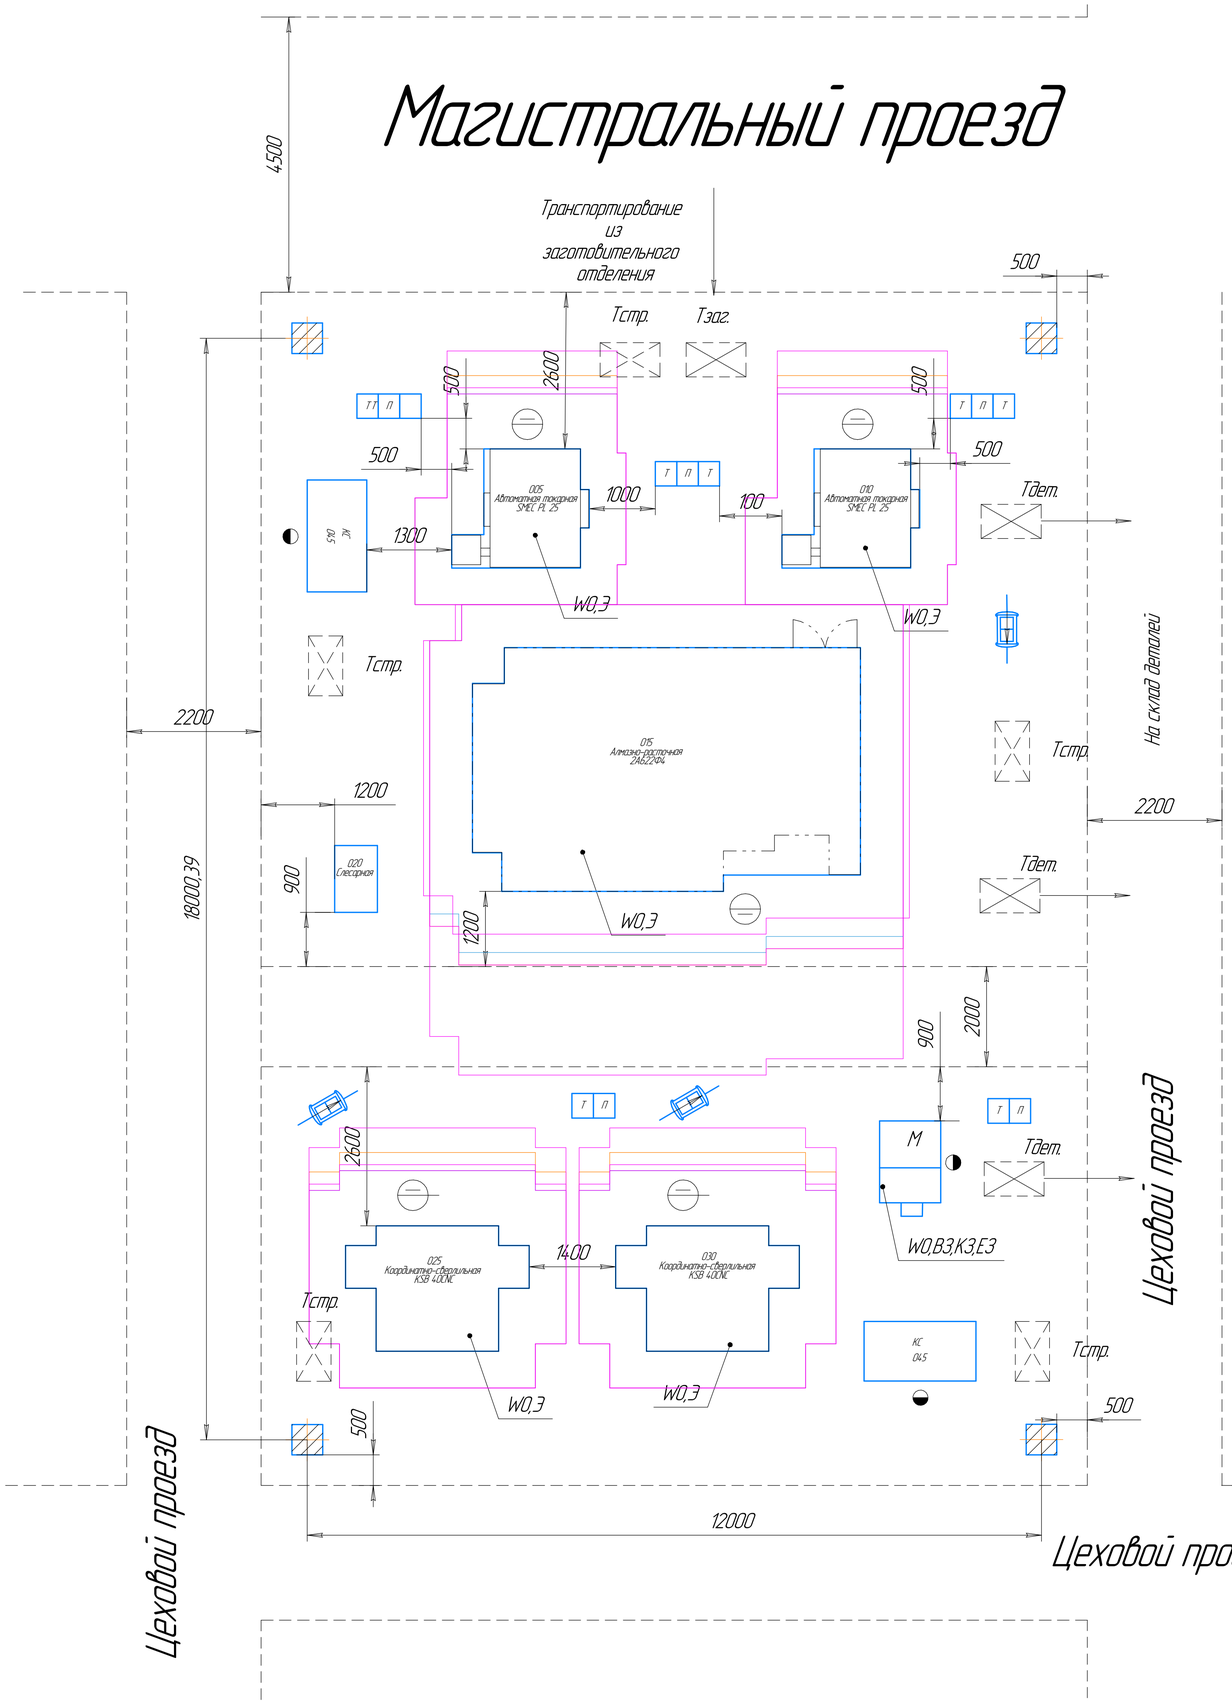

Условное обозначение:

- место под тару
- КС – контрольный стол
- В – верстак
- Т – тумбочка
- П – подставка под приспособление
- рабочее место
- заготовка – деталь
- бескрановая колонна
- тележка транспортная

Э – эмульсия
В3 – холодная вода производственная
Е3 – сжатый воздух
К3 – слив воды от оборудования в канализацию
W0 – подвод электроэнергии

Удельная производственная площадь – 35 м^2
Производственная площадь участка – 175 м^2
Вспомогательная площадь участка – 44 м^2
Общая площадь участка – 219 м^2
Средний коэффициент загрузки – 0,29

					711219-Цех 00-2112-ТХ.10.00	
Изм.	Лист	№ докум.	Подп.	Дата	Планировка участка Механической обработки	Лит. / Масса / Масштаб: 1:50
Разраб.						
Пров.						Лист / Листов: 1
Т.контр.						ООО «Не по ГОСТу, но попадает»
Н.контр.						
Утв.						

Копировал — Формат А1

Перв. примен. | Справ. № | Подп. и дата | Инв. № дубл. | Взам. инв. № | Подп. и дата | Инв. № подл.