




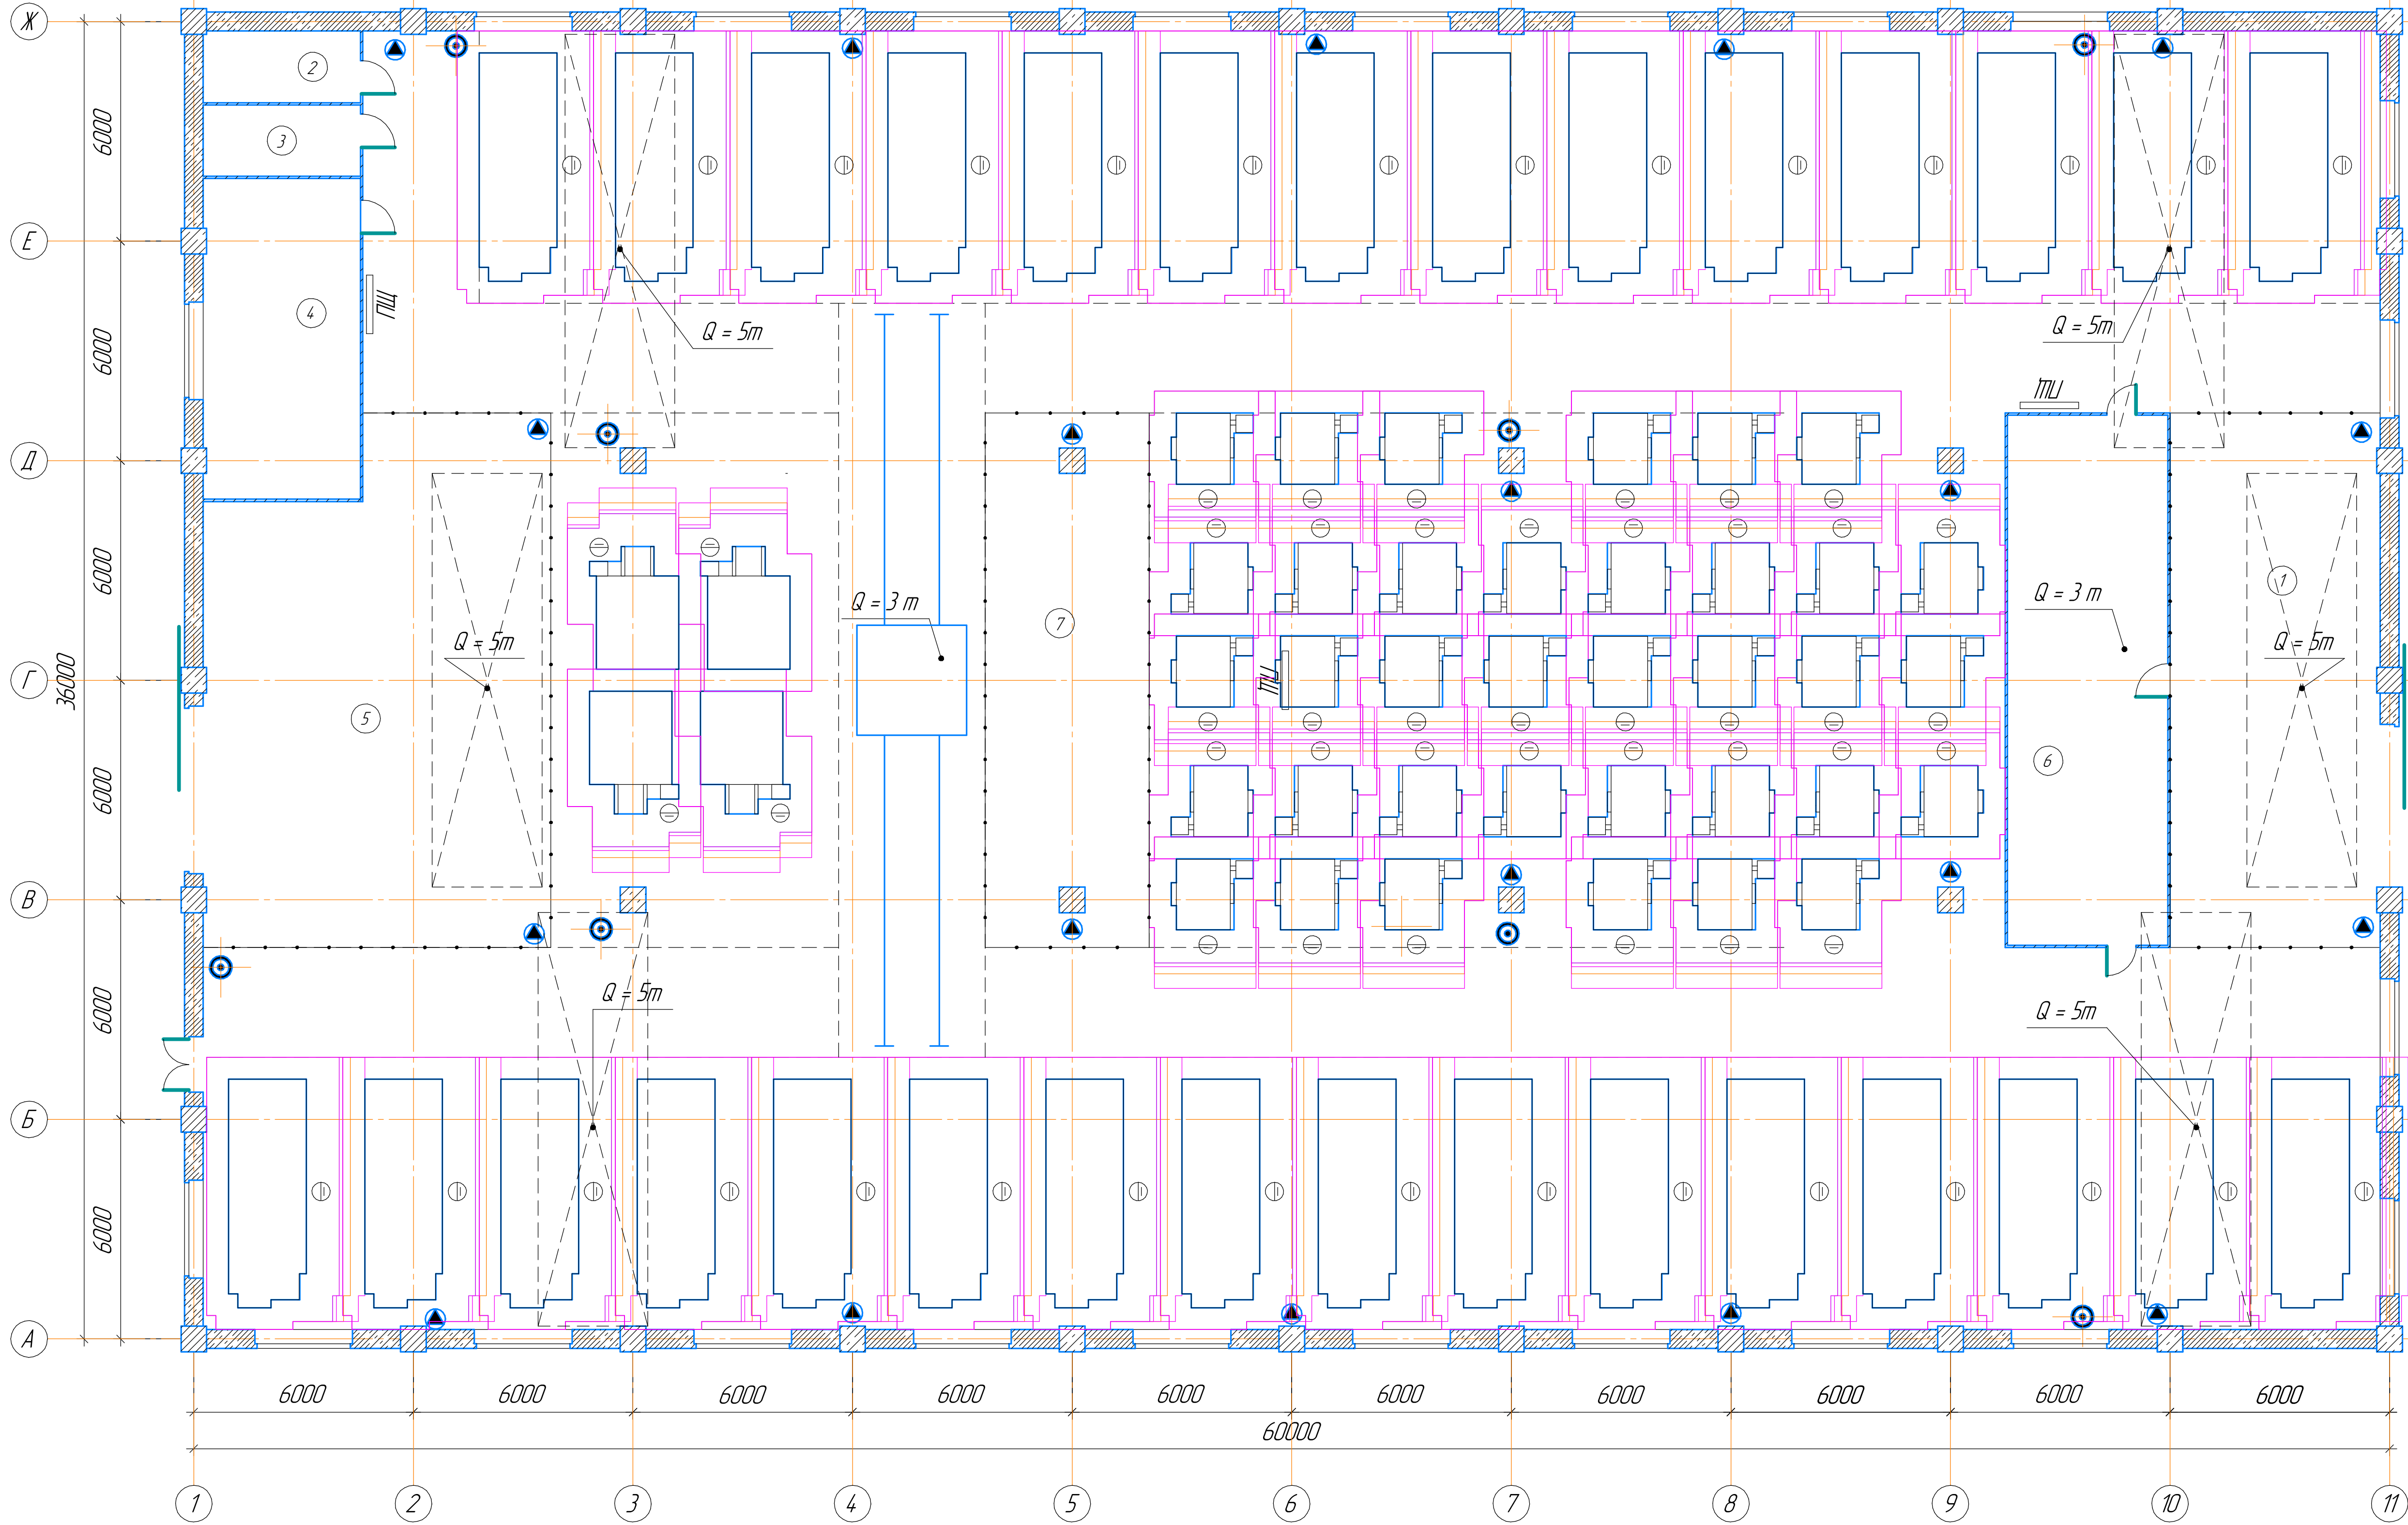


Условные обозначения:

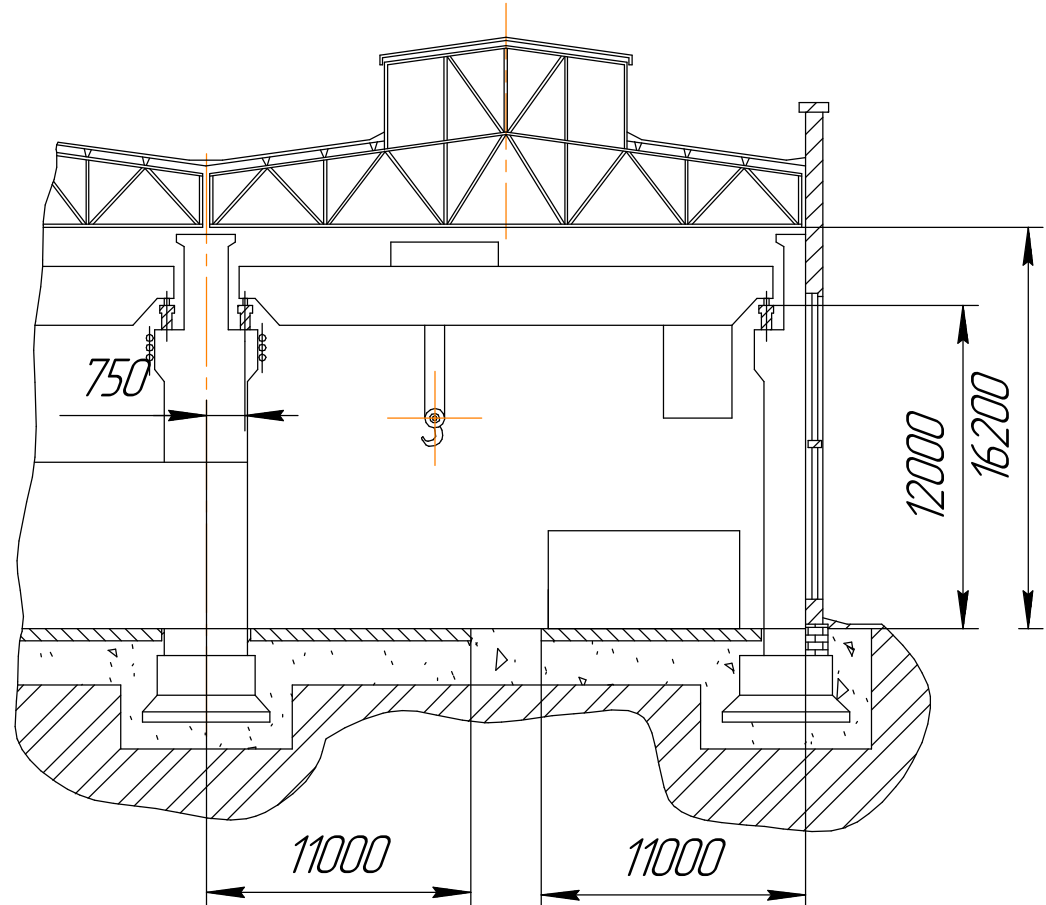

- ворота откатные
- кран мостовой
- ПЩ
- пожарный щит
- пожарный гидрант
- огнетушитель
- ворота распашные
- окно в стене
- одностворчатая дверь

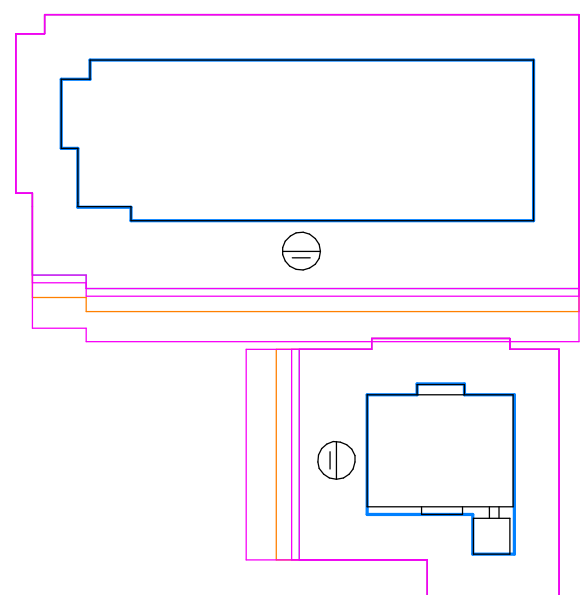

- токарный станок DMG CTX beta 2000

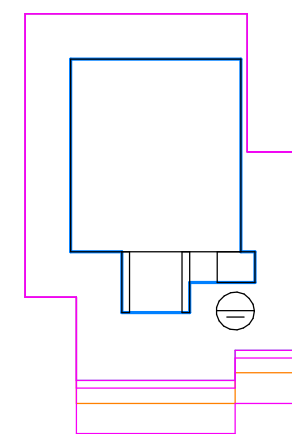

- фрезерный станок DMG DMU 80 eVo

- расточной станок УЦИ 2431СФ10

Номер помещения	Наименование	Площадь, м ²	Кат. помещения
1	Склад материалов и заготовок	203,47	
2	Санузел женский	8,46	
3	Санузел мужской	8,34	
4	Инструментально-раздаточная кладовая	31,6	
5	Склад готовых деталей	150,39	
6	Контрольное отделение	77,55	
7	Склад межоперационных деталей	64,81	

Изм.	Лист	№ докум.	Подп.	Дата
Разраб.				
Проб.				
Т.контр.				
Н.контр.				
Утв.				

711219-Цех 00-2112-TX.1100		
Планировка цеха		
Лит.	Масса	Масштаб
Лист 1	Листов 2	1:1
ООО «Болт и Молот»		
Копировал		
Формат А1		