
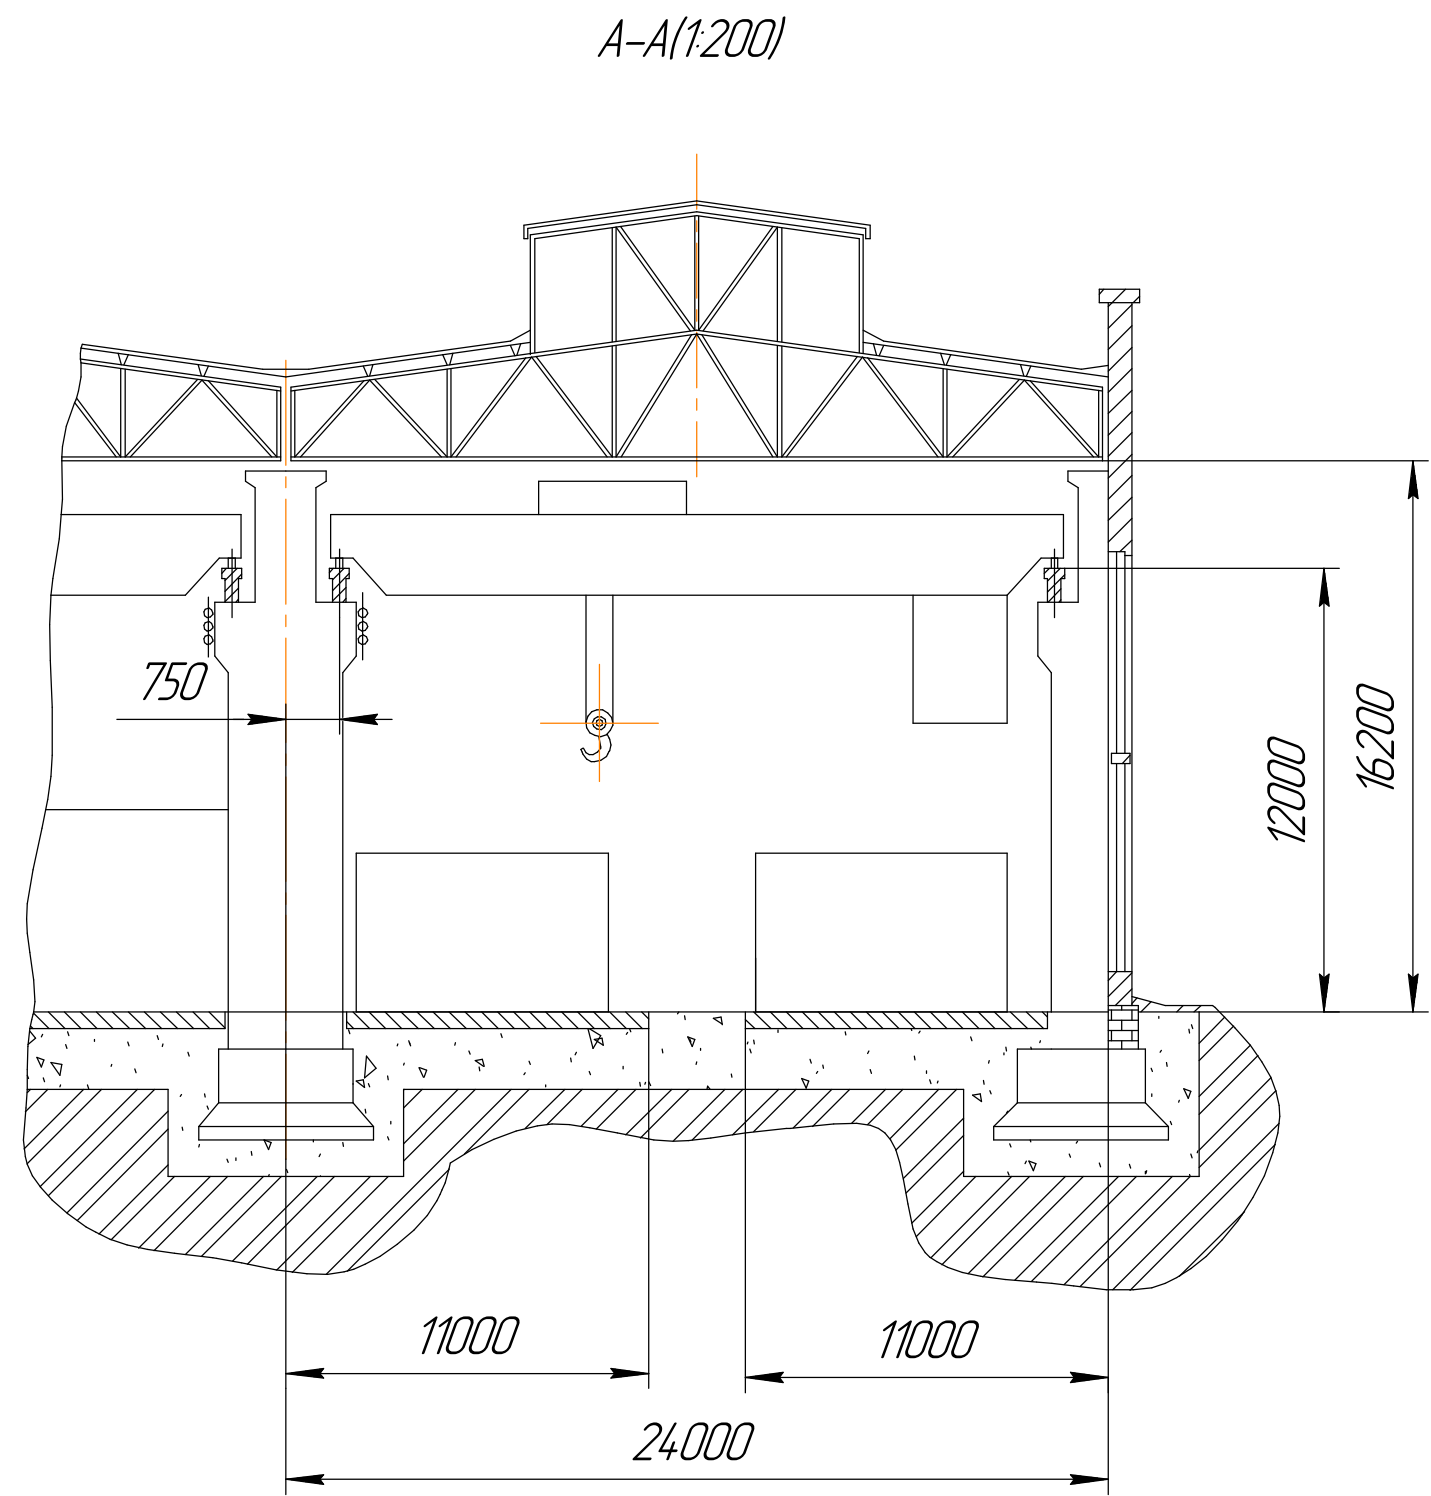


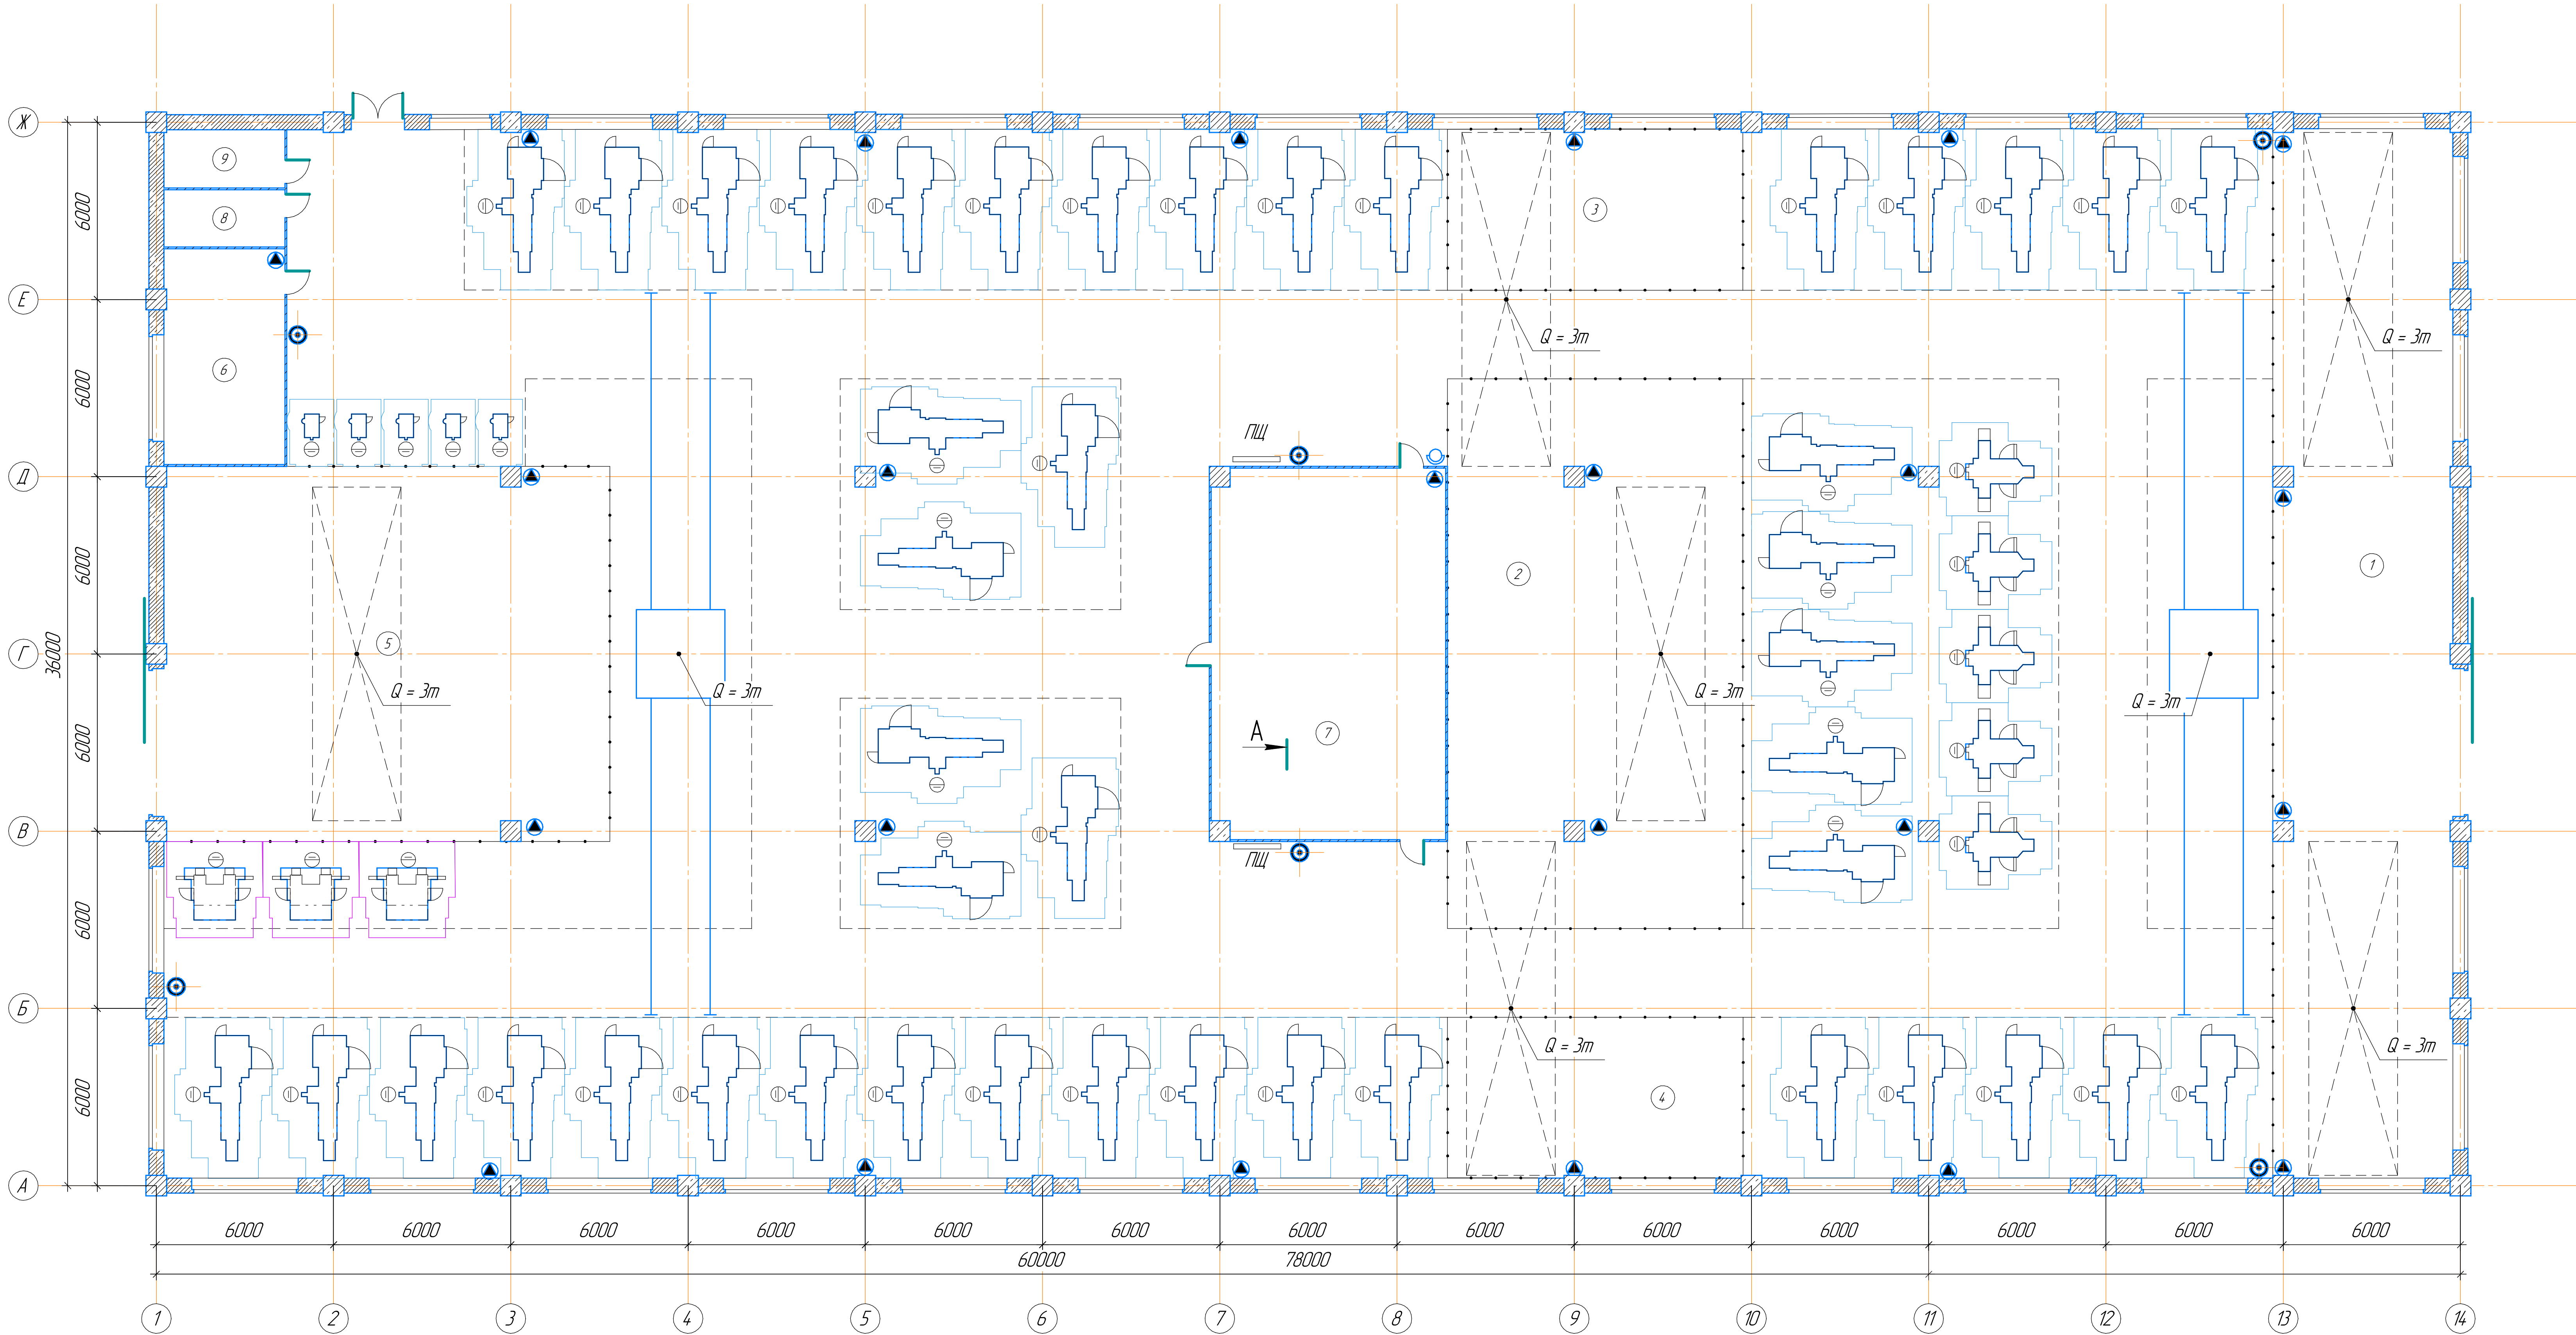

Условные обозначения:

- ворота открытые
- кран мостовой
- пожарный щит
- пожарный гидрант
- огнетушитель
- ворота распашные
- окно в стене
- однастворчатая дверь
- Токарный станок 1М63Ф101
- Сверлильный станок 2Н118
- Шлифовальный станок 35'51
- Фрезерный станок 6Р12

Номер помещения	Наименование	Площадь, м ²	Кот. помещ.
1	Склад материалов и заготовок	213,01	
2	Склад промежуточных деталей	185,15	
3	Склад промежуточных деталей	54,44	
4	Склад промежуточных деталей	54,36	
5	Склад готовых деталей	190,53	
6	Инструментально-раздаточная кладовая	29,88	
7	Контрольного отделения	99,07	
8	Санузел женский	7,95	
9	Санузел мужской	8,07	

711219-Цех 00-2112-TX.12.00				Лит. Масса Масштаб		
Планировка цеха				11		
				Лист Листов 1		
				ООО «По месту подполучения»		
				Формат А2х3		