





711219-Цех 00-2112-TX.14.00

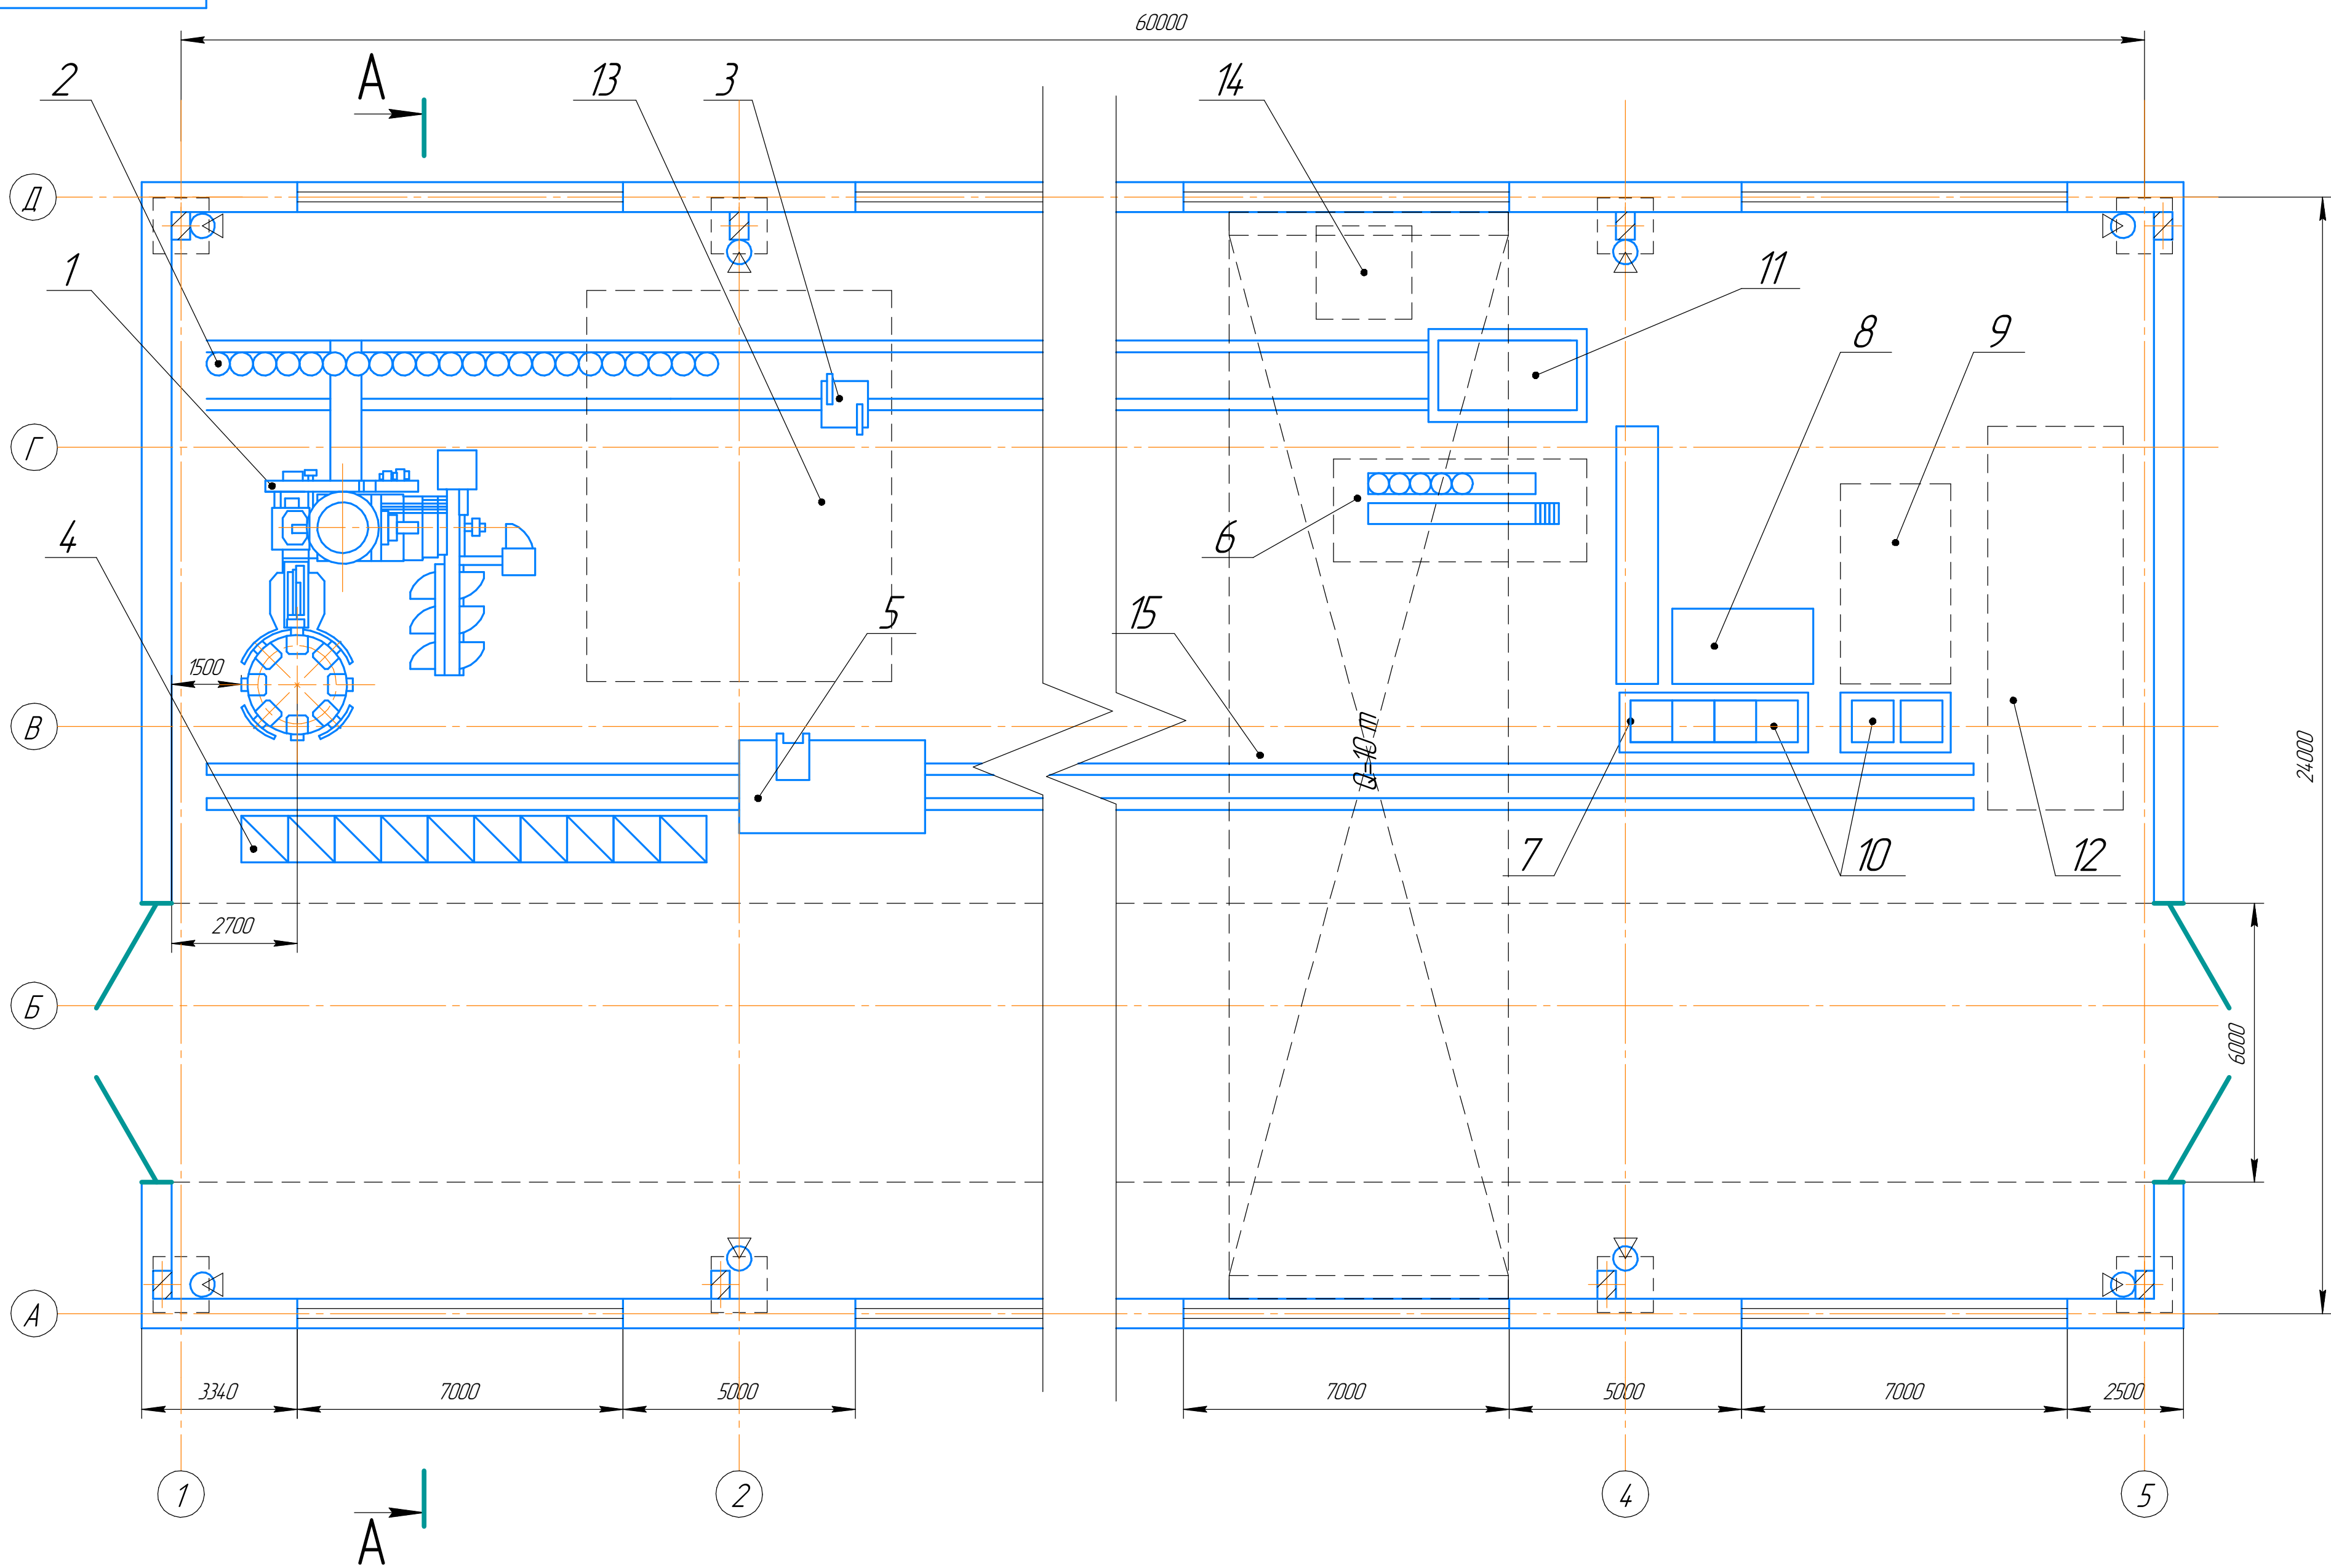

Структурная схема ГАЗ

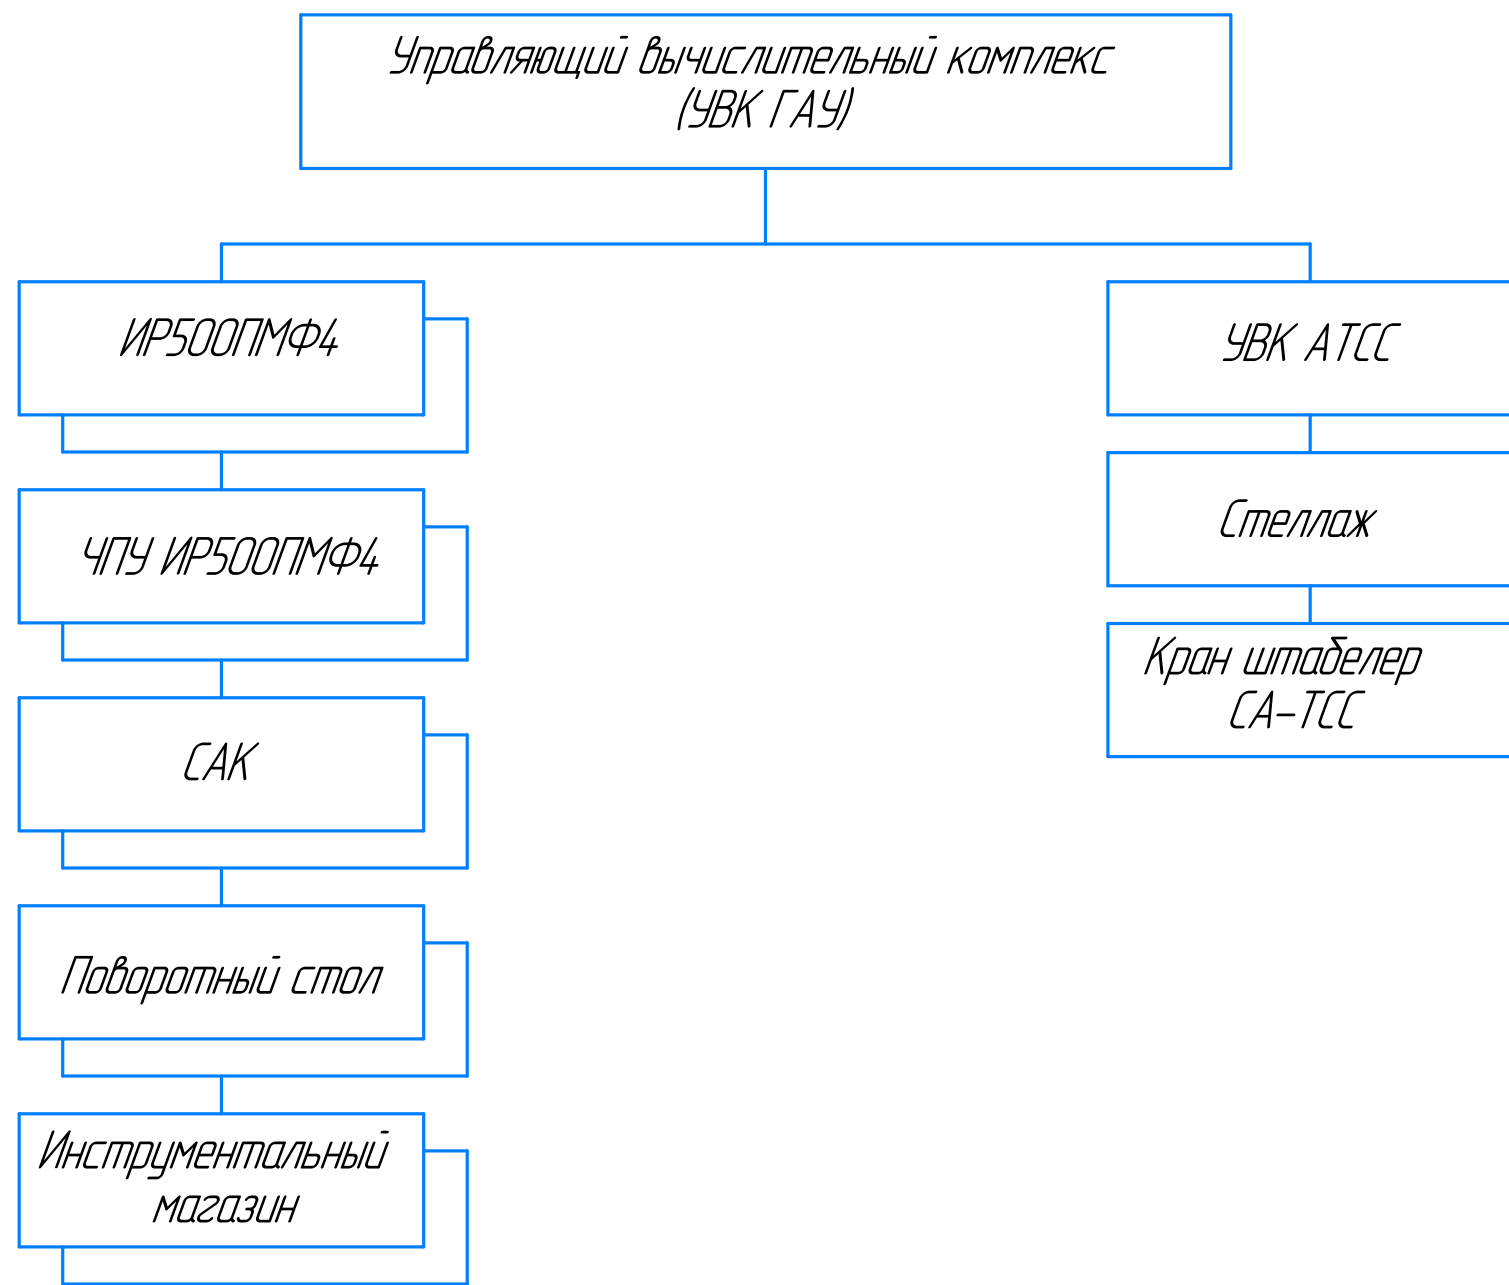

Уровень автоматизации всех систем ГАЗ

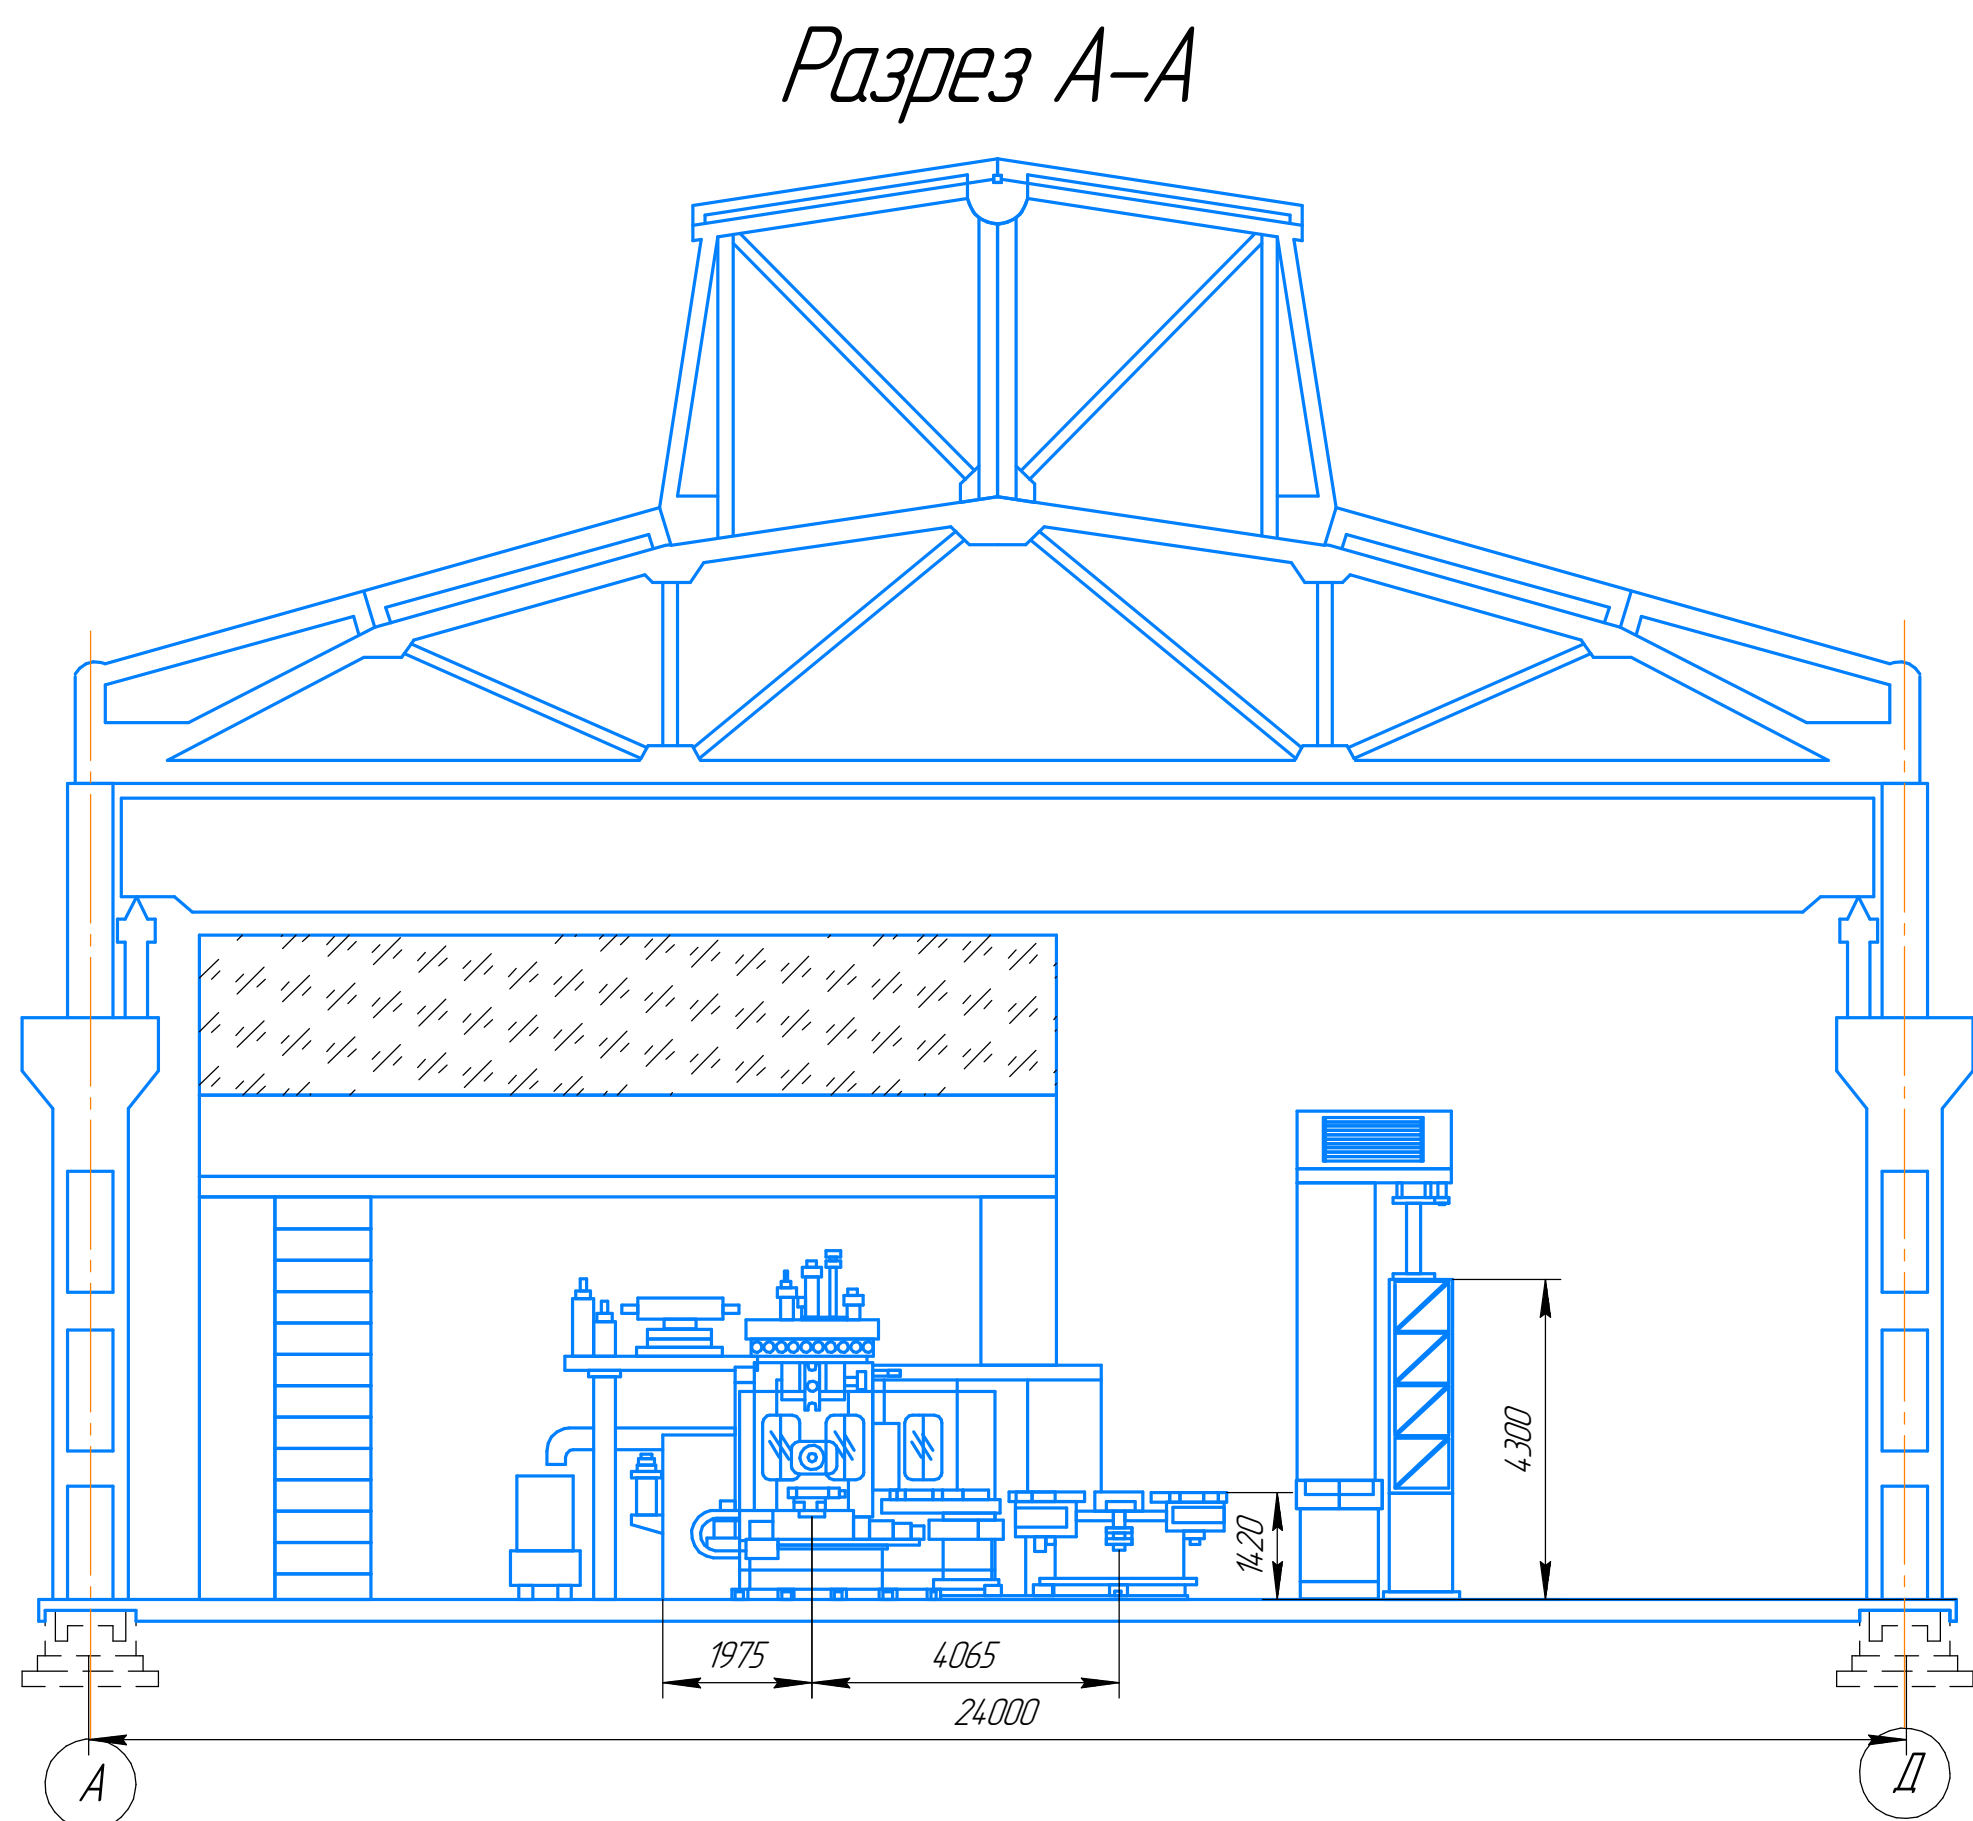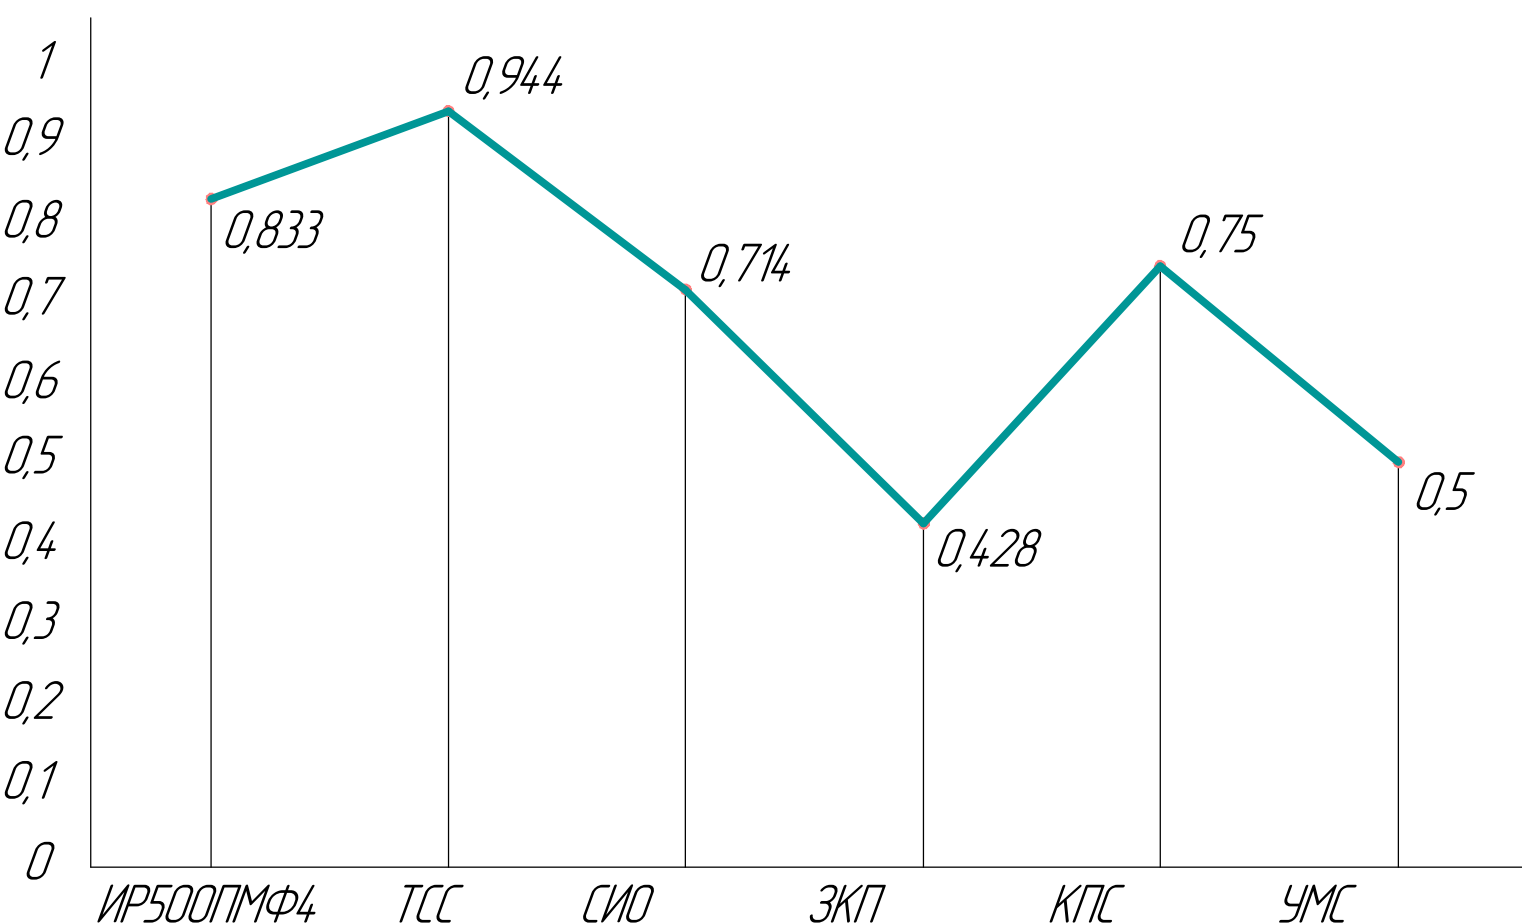

Формат	Зона	Позиция	Обозначение	Наименование	Количество	Примечание
		1	ИР500ПМФ4	Станок	1	
		2		Склад режущего инструмента	1	
		3	ТР - 0,5	Инструментальный робот	1	
		4	СТ - 0,25	Склад палет	1	
		5	СА - ТСС - 0,5	Кран - штабелер	1	
		6		Участок подготовки режущего инструмента	1	
		7	М1500Е	Моечная машина	1	
		8	Carl Zeiss PRISMO navigator	Координатно-измерительная машина	1	
		9		Участок подготовки палет	1	
		10		Перегрузочное устройство	2	
		11	ТР - 1,0	Рабочая рама	1	
		12		Склад готовой продукции	1	
		13		Операторная	1	
		14		Участок накопления стружки	1	
		15		Мостовой кран грузоподъемностью 10 тонн	1	

711219-Цех 00-2112-TX.14.00				Лит. Масса Масштаб		
Планировка участка ГПС				1:100		
Структурная схема ГАЗ				1		
Уровень автоматизации всех систем ГАЗ				000 «Универсальный Как-Нудель»		
Копировал				Формат А1		